План -4 этажа на отметке -15,000
М 1 : 200

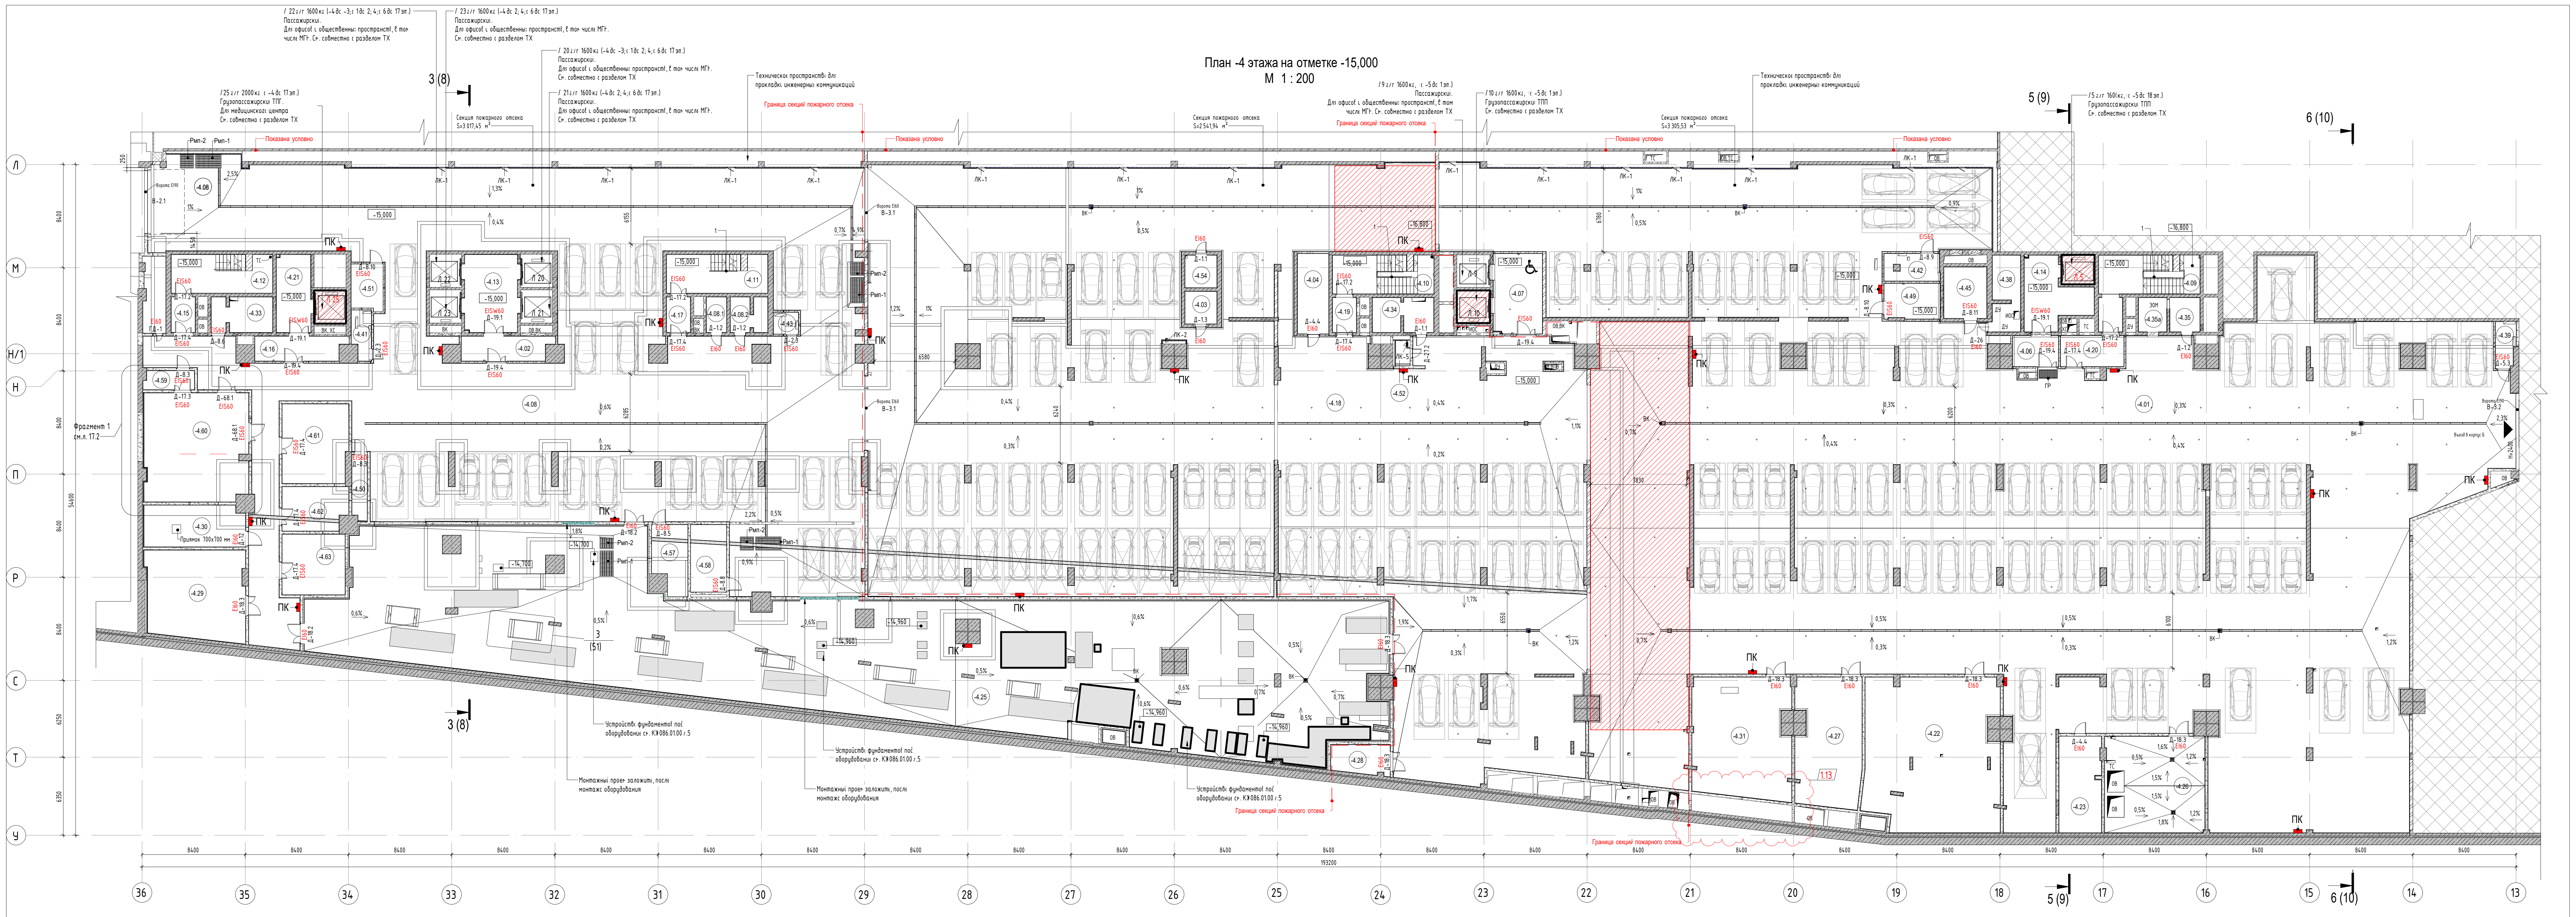

Экспликация помещений -4 этажа на отм. -15,000

Номер помещения	Наименование	Площадь, м²	Кат. пом.
01.Автостоянка			
-4.01	Помещение хранения автомобилей на 74 м/м	2815,80	В2
-4.08	Помещение хранения автомобилей на 24 м/м	1289,82	В2
-4.18	Помещение хранения автомобилей на 57 м/м	1960,49	В2
		6066,11	
14.Вспомогательные помещения			
-4.04	Помещение хранения пожарного инвентаря	17,06	В4
-4.38	Помещение хранения пожарного инвентаря	13,31	В4
-4.54	Помещение хранения пожарного инвентаря	6,91	В4
-4.59	Хранение ТМЦ	6,35	В4
-4.60	Помещение проведения инструктажа	74,56	
-4.61	Складское помещение отдела ИТ поддержки спецобъектов и спецрешений МЦТП	34,63	В3
-4.62	Складское помещение отдела ИТ поддержки аудио видео систем МЦТП	18,60	В3
-4.63	Складское помещение отдела приоритетной поддержки пользователей ПЦП МЦТП	25,64	В3
		197,06	
15.1Санузлы			
-4.52	Санузел	2,04	
		2,04	
15.Места общего пользования			
-4.02	Тамбур-шлюз	14,58	
-4.06	Тамбур-шлюз	9,57	
-4.07	Лифтовый холл/ тамбур-шлюз	26,43	

1.11

1.11

Экспликация помещений -4 этажа на отм. -15,000

Номер помещения	Наименование	Площадь, м²	Кат. пом.
-4.09	Лестничная клетка 2	32,14	
-4.10	Лестничная клетка 3	26,37	
-4.11	Лестничная клетка 4	26,39	
-4.12	Лестничная клетка 5	26,39	
-4.13	Лифтовый холл	27,76	
-4.14	Лифтовый холл	23,59	
-4.15	Тамбур-шлюз	5,90	
-4.16	Тамбур-шлюз	14,94	
-4.17	Тамбур-шлюз	5,90	
-4.19	Тамбур-шлюз	5,78	
-4.20	Тамбур-шлюз	13,23	
-4.21	Лифтовый холл	17,73	
		276,70	
16.Инженерные помещения			
-4.03	Помещение уборочной техники	6,94	В4
-4.08.1	Тех. помещение прокладки инж.коммуникаций	4,85	В4
-4.08.2	Электрощитовая	8,39	В4
-4.22	Венткамера	133,37	В3
-4.23	Электрощитовая	27,13	В3
-4.25	Холодильный центр	912,15	Д
-4.26	Венткамера	58,95	Д

1.11

Экспликация помещений -4 этажа на отм. -15,000

Номер помещения	Наименование	Площадь, м²	Кат. пом.
-4.27	Венткамера	55,19	В2
-4.28	Электрощитовая общедомовая	11,48	В3
-4.29	Венткамера	57,64	В3
-4.30	Венткамера	27,93	Д
-4.31	Венткамера	77,32	В2
-4.33	Электрощитовая	14,17	В3
-4.34	Электрощитовая	14,17	В3
-4.35	Электрощитовая	7,09	В4
-4.35а	Электрощитовая	6,51	В4
-4.39	Помещение вертикальных коммуникаций ИТ и СС	6,07	В4
-4.41	Помещение вертикальных коммуникаций ИТ и СС	5,97	В4
-4.42	Помещение вертикальных коммуникаций ИТ и СС	9,56	В4
-4.43	Помещение вертикальных коммуникаций ИТ и СС	3,67	В4
-4.45	Помещение для оборудования кондиционирования и АУГПТ	15,40	В3
-4.49	Помещение "КУ АСО"	13,28	В3
-4.50	Помещение для пожарного инвентаря	6,64	В4
-4.51	Помещение слаботочных систем	9,49	В4
-4.57	Помещение для размещения оборудования кондиционирования и АУГПТ	14,80	В3
-4.58	Помещение "КУ АСО"	15,98	В3
		1524,14	
Итого		8066,05	

1.11

Ведомость машиномест -4 этаж

Наименование	Кол-во, шт.
Машино-место 5300х2500мм. Средний класс	109
Машино-место 5300х2500мм. Малый класс	19
Машино-место зависимое 5300х2500мм. Малый класс	4
Машино-место зависимое 5300х2500мм. Средний класс	18
	150

Условные обозначения:

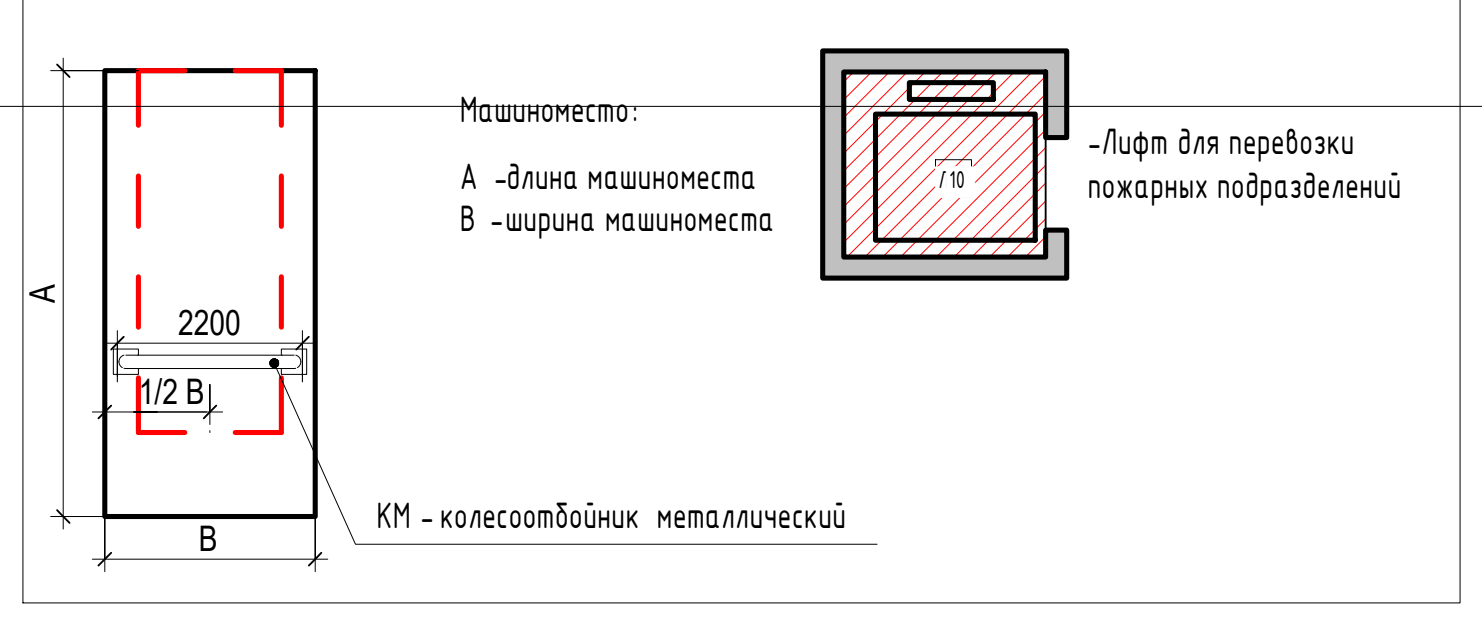

Машиноместо:

А -длина машиноместа

В -ширина машиноместа

-Лифт для перевозки пожарных подразделений

- Гр - Грязезащитная решетка
- 1 - Тип лестничного ограждения
- 🟥 - Пожарный шкаф
- ← 0,3% - Направление уклона пола
- ▨ Зона свободная от пожарной нагрузки

Схема блокировки корпусов

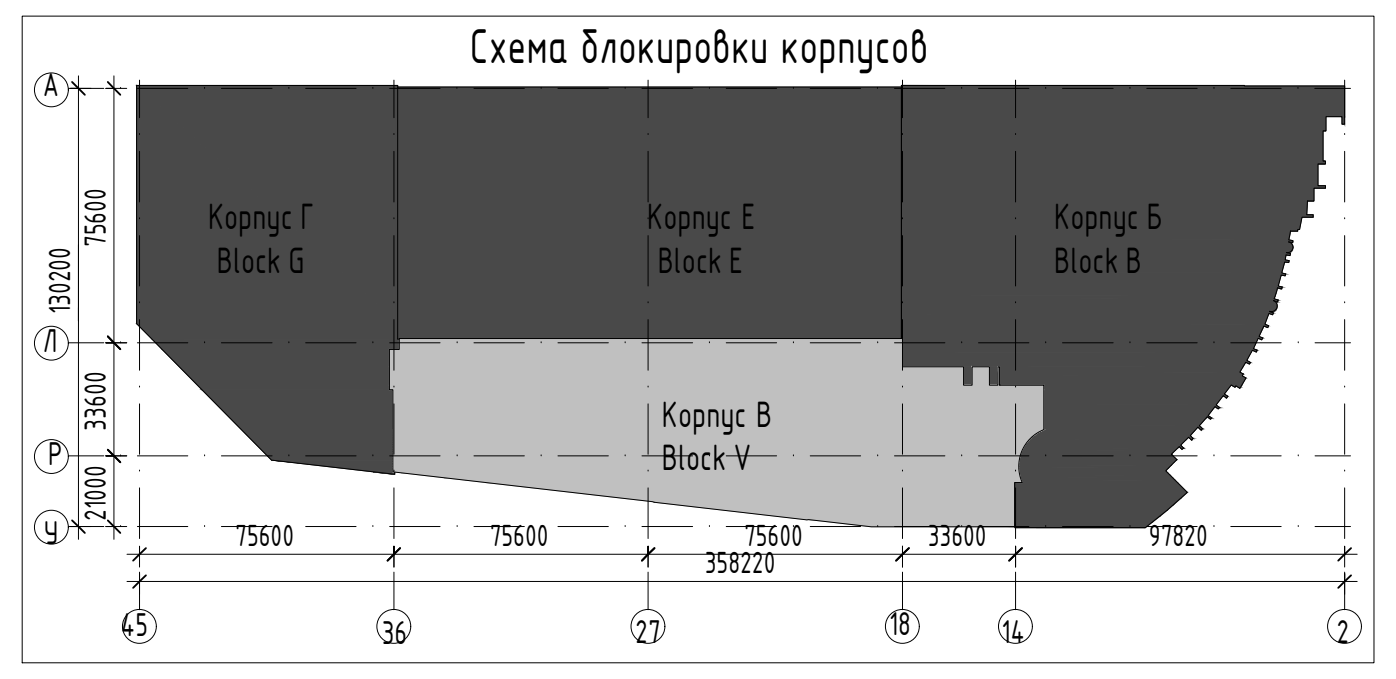

1. Лист смотреть совместно с л. 7-11.
2. Схемы дверных блоков и спецификацию элементов заполнения проемов смотреть на л. 12.
3. Ведомость отделки помещений смотреть на л. 37.
4. План полов смотреть на л. 26, 26.1, 26.2, 26.3, 26.4. Экспликация полов дана на л. 27.
5. Стояки и воздуховоды зашить по месту. Расход материала смотри спецификацию расхода материалов на л. 24 настоящего альбома.
6. Против ревизий на стояках канализации в коробах зашивки предусмотреть по месту установку нажимных люков под плитку размером 300х400h на высоте 800 мм от чистого пола в помещениях с отделкой стен плиткой; декоративных нажимных люков в помещениях со стенами под покраску.
7. Коммуникации, зашитые ГКЛ и кирпичной кладкой, оборудовать лючками с нажимным механизмом, согласно пункта 6. Замком оборудовать двери для входа в ниши коммуникаций.
8. Направляющие ЗД-1 смотри раздел: Строительное задание Корпус В от "Гарантэнерго" Шифр: 5КС-АТК-СЗ.
9. Ведомость окраски стен помещний автостоянки см. л. 37.
10. Выполнить затирку цементно-песчаным раствором до достижения ровной гладкой поверхности, как по горизонтали, так и по вертикали с последующим нанесением одного слоя шпатлевки.
11. Расстановку машиномест их привязки, узел устройства колесоотбойников и их точное размещение см. СБД-КУТ03-КМП-2-25-Р-100-ТХ.01.00. Технологические решения. Подземная автостоянка.
12. Корректировка данного листа выполнена на основании исходных данных раздела АР. СБД-1276-ПК-КУТ03-0000-АР01.00, выполненной компанией ТПО "Прайд".
13. Маркировка и грузоподъемность лифтов указаны на основании Приложения №5 "Схема вертикального транспорта Корпуса В" к официальному письму от ООО "СБД" от 06.02.2024 № КУТ06-06_392 "О направлении требований к корректировке РД по -1, -2, -3, -4, -5 эт."
14. Ограждение "ОГО-1" выполнить согласно указаным размерам 2500х580 (h=1000мм) и согласно документации "СЭ 18245-05.26- ПП". Смотреть совместно с листом 18 данного комплекта.

С выпуском данного листа аннулировать лист №3 Прайдекс Констракшн шифр PR-200.СБВ.АР01.00 (и

0,000 = 147,500

Согласовано

Взам. инв. №

Подп. и дата

Инв. № подл.

1		Изм.	3932/26		06.26
Изм.	Кол уч.	Лист	№ док.	Подпись	Дата
Разработал		Рыбальченко			24.03.26
Проверил		Бугакова			24.03.26
ГАП		Пичурова			24.03.26
ГИП		Хорлуков			24.03.26
Н.контроль		Пичурова			24.03.26

КУТ03-Р-ПИР-2-26-100 - АР01.01.00

Реконструкция делового комплекса в составе корп. «А», «Б», «В», «Г», «Е» с единой стилобатной подземной частью и устройством надземной объединительной аркады по адресу: пересечение Кутузовского проспекта и улицы Кульнева, район Дорогомилово, Западный административный округ города Москвы

Архитектурные решения. Подземная автостоянка (Стилобат)

Стадия	Лист	Листов
Р	3	

План -4 этажа на отметке -15,000

MARKS ENGINEERING

Формат А2х3