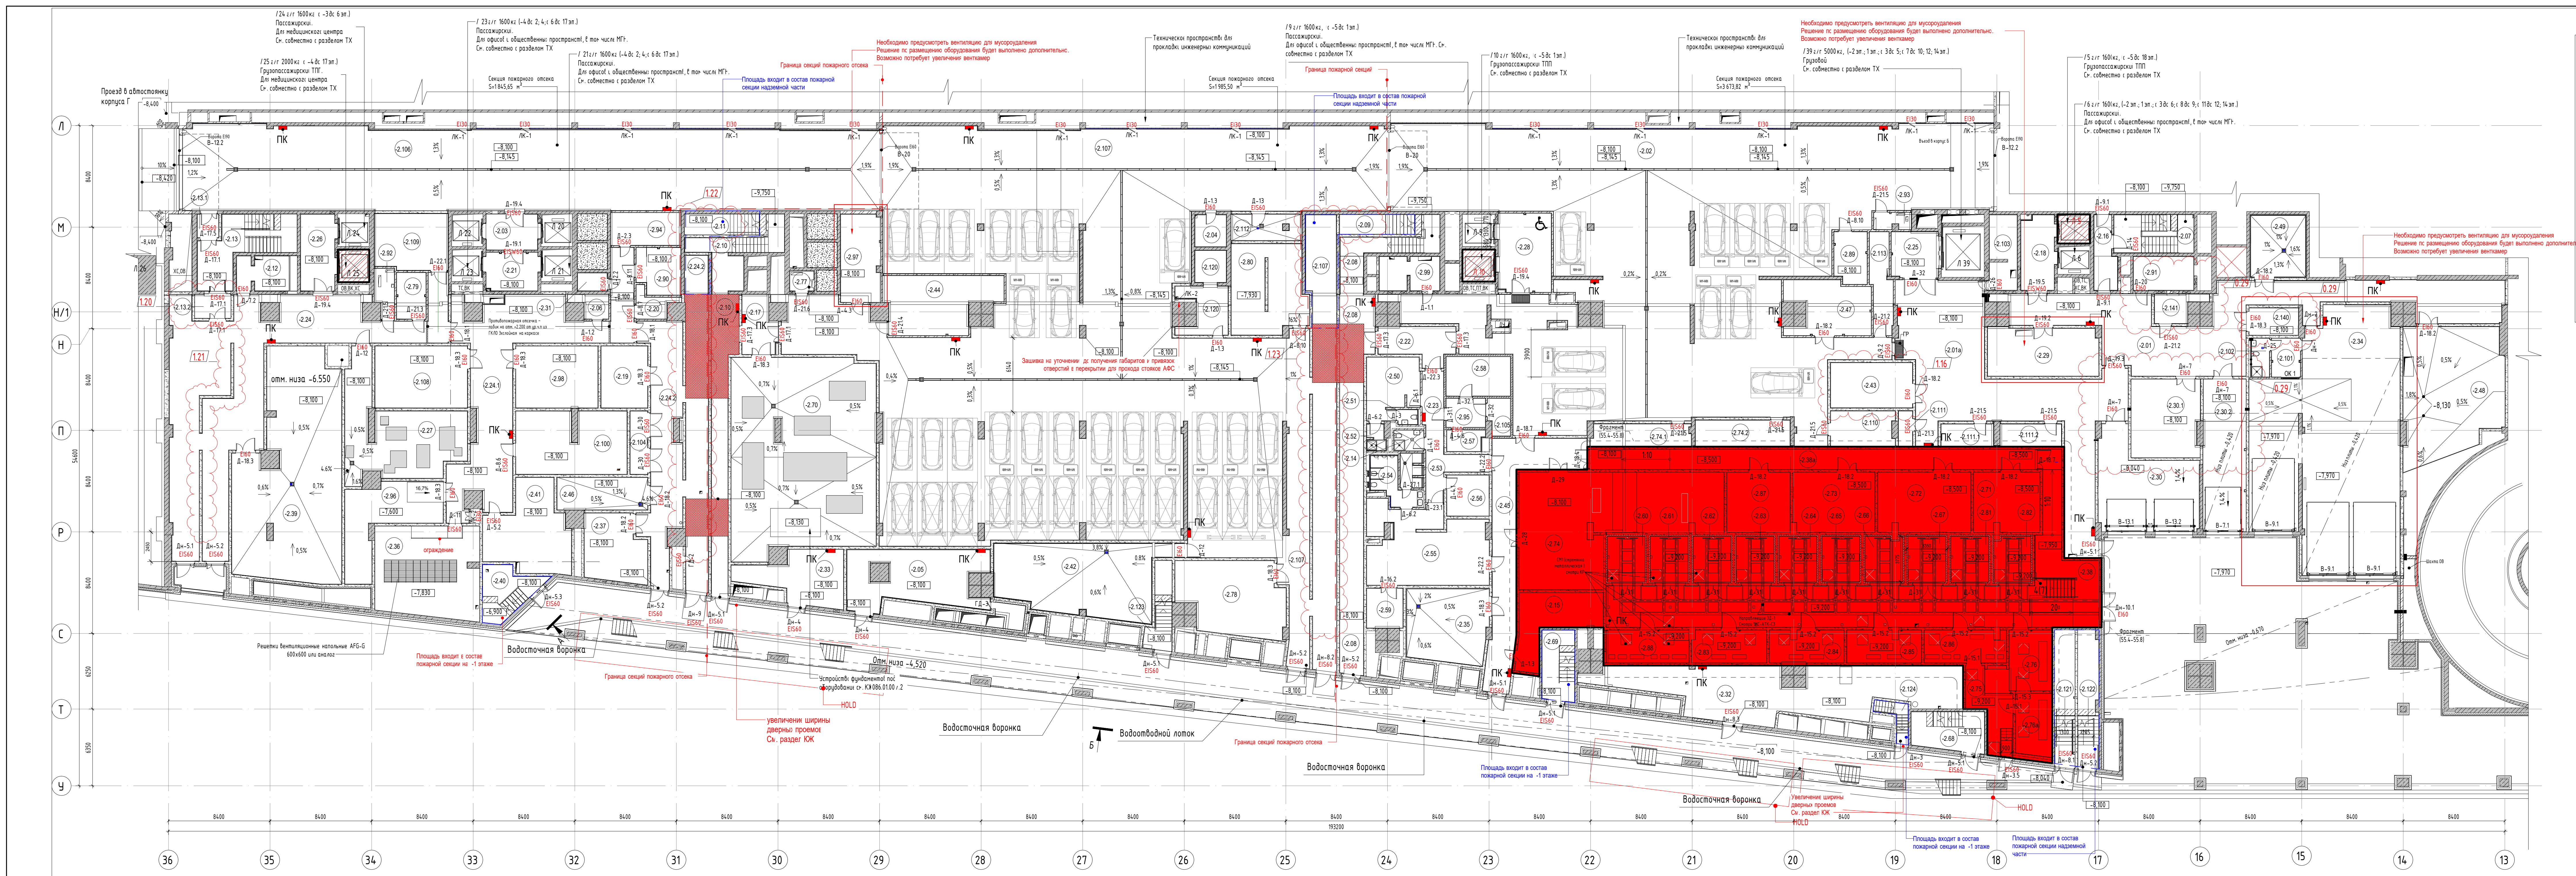
Проезд в автостоянку корпуса Г
Л
М
Н/1
Н
П
Р
С
Т
У
ПК
отм. низа -6.550
Водосточная воронка
Водоотводный лоток
Решетка вентиляционная напольная АРБ-G 600х600 или аналог
Площадь входит в состав пожарной секции на -1 этаже
Площадь входит в состав пожарной секции надземной части
Граница секций пожарного отсека
Увеличение ширины дверных проемов См. раздел КЖ
HOLD
8400
193200
36
35
34
33
32
31
30
29
28
27
26
25
24
23
22
21
20
19
18
17
16
15
14
13

## Условные обозначения:

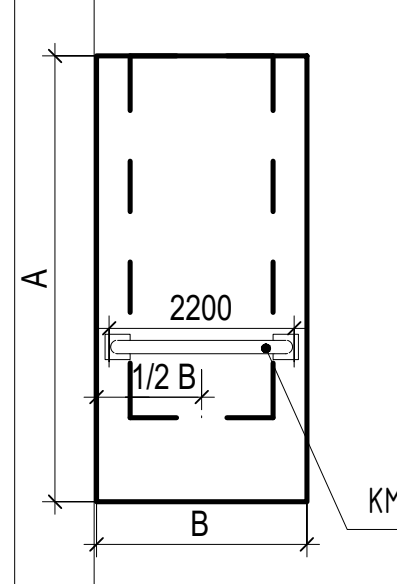

Машиноместо:
A -длина машиноместа
B -ширина машиноместа

КМ - колесоотбойник металлический

-Лифт для перевозки пожарных подразделений

♿ М4 - Группа мобильности М4
♿ М1-М3 - Группа мобильности М1-3

Гр - Грязезащитная решетка
1 - Тип лестничного ограждения
🟥 - Пожарный шкаф
← 0,3% - Направление уклона пола
▨ Зона свободная от пожарной нагрузки

▨ Зона двойного перекрытия (на уточнении)
🟥 Помещения ЭнергоЦентра

## Экспликация помещений -2 этажа на отм. -8,100

| Номер помещения | Наименование | Площадь, м² | Кат. пом. |
|---|---|---|---|
| 01.Автостоянка | | | |
| -2.02 | Помещение хранения автомобилей на 12 м/м | 802,58 | В2 |
| -2.106 | Помещение автостоянки | 390,03 | В2 |
| -2.107 | Помещение хранения автомобилей на 29 м/м | 1240,70 | В2 |
| | | 2433,32 | |
| 12.Предприятия общественного питания | | | |
| -2.01 | Коридор | 143,84 | - |
| -2.01а | Коридор | 152,78 | - |
| -2.30 | Зона загрузки хоз. служб здания | 56,30 | В4 |
| -2.30.1 | Помещение загрузки предприятия питания | 36,56 | - |
| -2.30.2 | Зона загрузки | 44,84 | В2 |
| -2.140 | Инвентарная | 9,29 | В3 |
| -2.141 | Помещение уборочного инвентаря | 7,98 | |
| | | 451,59 | |
| 14.Вспомогательные помещения | | | |
| -2.06 | Помещение хранения пожарного инвентаря | 5,07 | В4 |
| -2.14 | Помещение уборочного инвентаря | 4,31 | В4 |
| -2.15 | Комната приема пищи | 26,66 | - |
| -2.23 | Коридор | 22,92 | - |
| -2.38 | Коридор | 166,33 | - |
| -2.38а | Коридор | 61,21 | - |
| -2.50 | Раздевалка женская | 20,81 | - |
| -2.51 | Санузел женский | 2,01 | - |
| -2.52 | Душевая женская | 3,21 | - |
| -2.53 | Душевая мужская | 5,44 | - |
| -2.54 | Санузел мужской | 10,55 | - |
| -2.55 | Раздевалка мужская | 59,47 | - |
| -2.56 | Помещение хранения постовой одежды | 11,97 | В3 |
| -2.57 | Хранение ТМЦ | 5,33 | В4 |
| -2.58 | Помещение для заряжания/разряжания оружия | 17,53 | |
| -2.59 | Помещение сушки | 9,99 | - |
| -2.74.1 | Раздевалка | 15,05 | |
| -2.74.2 | Раздевалка | 17,12 | |
| -2.87 | Помещение хранения пожарного инвентаря | 25,98 | - |
| -2.95 | Помещение для выдачи оружия | 7,91 | |
| -2.102 | Санузел | 4,81 | - |
| -2.105 | Помещение для хранения оружия и патронов | 5,50 | |
| -2.111.1 | Раздевалка | 8,11 | |
| -2.111.2 | Раздевалка | 9,45 | |
| -2.120 | Помещение уборочного инвентаря | 21,11 | В4 |
| | | 547,86 | |
| 15.Места общего пользования | | | |
| -2.03 | Тамбур-шлюз | 12,81 | - |
| -2.07 | Лестничная клетка 2 | 20,81 | - |
| -2.08 | Лестничная клетка 3 | 91,78 | - |
| -2.10 | Лестничная клетка 4 | 60,83 | - |
| -2.13 | Лестничная клетка 5 | 30,18 | - |
| -2.13.1 | Тамбур-шлюз | 3,51 | - |
| -2.13.2 | Тамбур-шлюз | 6,03 | |
| -2.16 | Тамбур-шлюз | 10,27 | - |
| -2.17 | Тамбур-шлюз | 12,95 | - |
| -2.18 | Лифтовый холл/ тамбур-шлюз | 16,56 | - |
| -2.21 | Лифтовый холл | 14,53 | - |
| -2.22 | Тамбур-шлюз | 16,82 | - |
| -2.24 | Коридор | 185,94 | - |
| -2.24.1 | Коридор | 116,60 | - |
| -2.24.2 | Коридор | 108,09 | - |
| -2.25 | Лифтовый холл/ тамбур-шлюз | 14,69 | - |
| -2.26 | Лифтовый холл/ тамбур-шлюз | 18,23 | - |
| -2.28 | Лифтовый холл/ тамбур-шлюз | 28,65 | - |
| -2.40 | Лестничная клетка 8 | 16,58 | - |
| -2.45 | Коридор | 57,89 | - |
| -2.68 | Лестничная клетка 6 | 19,03 | - |
| -2.69 | Лестничная клетка 7 | 15,63 | - |
| -2.121 | Лестничная клетка 12 | 18,32 | - |
| -2.122 | Лестничная клетка 11 | 19,08 | - |
| -2.123 | Лестничная клетка 9 | 11,94 | - |
| -2.124 | Лестничная клетка 10 | 4,99 | - |
| | | 932,71 | |
| 16.Инженерные помещения | | | |
| -2.04 | Помещение уборочной техники | 7,10 | В4 |
| -2.05 | Венткамера ДУ | 51,25 | В2 |
| -2.09 | Помещение для прокладки инженерных коммуникаций | 6,16 | - |
| -2.11 | Помещение для прокладки инженерных коммуникаций | 10,71 | - |
| -2.12 | Электрощитовая | 12,12 | В3 |
| -2.19 | Помещение для хранения запасов газ. баллонов и пожарного инвентаря | 19,87 | В3 |
| -2.20 | Помещение для фанкойла и Газ. балона | 5,96 | В3 |
| -2.27 | Насосная | 63,43 | В3 |
| -2.29 | Помещение для накопителя крупных отходов | 36,58 | В3 |
| -2.31 | ЭОМ | 3,74 | В4 |
| -2.32 | Венткамера | 103,81 | В3 |
| -2.33 | Венткамера | 29,82 | В3 |
| -2.34 | Мусорокамера | 229,21 | В2 |
| -2.35 | Венткамера | 40,21 | В4 |
| -2.36 | Центральный коммутационный узел 2 | 64,08 | В3 |
| -2.37 | Венткамера подпора | 27,20 | Д |
| -2.39 | Венткамера | 144,64 | В3 |
| ~~-2.41~~ | ~~Электрощитовая ВРУ~~ | ~~42,14~~ | В3 |
| -2.42 | Венткамера | 77,02 | Д |
| -2.43 | Техническое помещение | 25,46 | В4 |
| -2.44 | Электрощитовая офисов | 39,77 | В3 |
| -2.46 | Венткамера | 20,27 | В2 |
| -2.47 | Венткамера | 28,38 | В2 |
| -2.48 | Техническое помещение | 83,97 | В3 |
| -2.49 | Венткамера | 23,30 | Д |
| -2.60 | Трансформаторная камера | 11,84 | В4 |
| -2.61 | Трансформаторная камера | 11,74 | В4 |
| -2.62 | Трансформаторная камера | 11,88 | В4 |
| -2.63 | Трансформаторная камера | 11,88 | В4 |
| -2.64 | Трансформаторная камера | 11,88 | В4 |
| -2.65 | Трансформаторная камера | 11,70 | В4 |
| -2.66 | Трансформаторная камера | 10,54 | В4 |
| -2.67 | Трансформаторная камера | 12,07 | В4 |
| -2.70 | Насосная пожаротушения | 189,70 | Д |
| -2.71 | ГРЩ-5В | 26,62 | В3 |
| -2.72 | ГРЩ-4В | 37,74 | В3 |
| -2.73 | ГРЩ-3В | 33,31 | В3 |
| -2.74 | ГРЩ-2В | 115,70 | В3 |
| -2.75 | Помещение ревизии инженерных коммуникаций | 15,66 | В3 |
| -2.76 | РУ-20кВ (2 секц.) | 17,68 | В3 |
| -2.76а | РУ-20кВ (1 секц.) | 15,28 | В3 |
| -2.77 | Помещение вертикальных коммуникаций СС и ИТ | 3,49 | В4 |
| -2.78 | Венткамера | 49,91 | В2 |
| -2.79 | Помещение пожарного инвентаря | 9,45 | В4 |
| -2.80 | Центральная аппаратная операторов сотовой связи | 43,87 | В3 |
| -2.81 | Трансформаторная камера | 11,88 | В4 |
| -2.82 | Трансформаторная камера | 11,29 | В4 |
| -2.83 | Распред устройство 20кВт | 16,53 | В3 |
| -2.84 | Распред устройство 20кВт | 16,26 | В3 |
| -2.85 | Распред устройство 20кВт | 16,27 | В3 |
| -2.86 | Распред устройство 20кВт | 17,93 | В3 |
| -2.88 | Распред устройство 20кВт | 18,80 | В3 |
| -2.89 | Кроссовая КУ АСО | 11,58 | В3 |
| -2.90 | Кроссовая КУ АСО | 13,79 | В3 |
| -2.91 | Электрощитовая | 13,70 | В3 |
| -2.92 | Помещение вертикальных коммуникаций ИТ и СС | 6,34 | В4 |
| -2.93 | Помещение вертикальных коммуникаций ИТ и СС | 3,93 | В4 |
| -2.94 | Помещение слаботочных систем | 15,80 | В3 |
| -2.96 | Венткамера(прецизионные кондиционеры) | 37,19 | В3 |
| -2.97 | Техпомещение вакуумного мусороудаления | 24,14 | В3 |
| -2.98 | Помещение ИБП | 34,97 | В3 |
| -2.99 | Электрощитовая офисов | 13,41 | В3 |
| -2.100 | Электрощитовая ВРУ | 46,99 | В3 |
| -2.101 | Помещение оператора мусорокамеры | 7,72 | - |
| -2.103 | Помещение для прокладки инженерных коммуникаций | 13,46 | - |
| -2.104 | Помещение для фанкойла и Газ. баллона | 7,67 | В4 |
| -2.108 | МЦТП | 39,34 | В3 |
| -2.109 | МЦТП | 28,34 | В3 |
| -2.110 | Помещение операторского ввода | 15,33 | В3 |
| -2.111 | Помещение для фанкойла и газ. баллона | 3,94 | В4 |
| -2.112 | Венткамера(прецизионные кондиционеры) | 12,64 | В3 |
| -2.113 | Помещение для фанкойла и АУГПТ | 14,06 | В3 |
| | | 2321,46 | |
| Итого | | 6686,94 | |

1.11

| Ведомость машиномест -2 этаж | |
|---|---|
| Наименование | Кол-во, шт. |
| Машино-место 5300х2500мм (МГН группы М1-М3) | 22 |
| Машино-место 5300х2500мм. Средний класс | 9 |
| Машино-место зависимое 5300х2500мм. Средний класс | 12 |
| | 43 |

### Схема блокировки корпусов

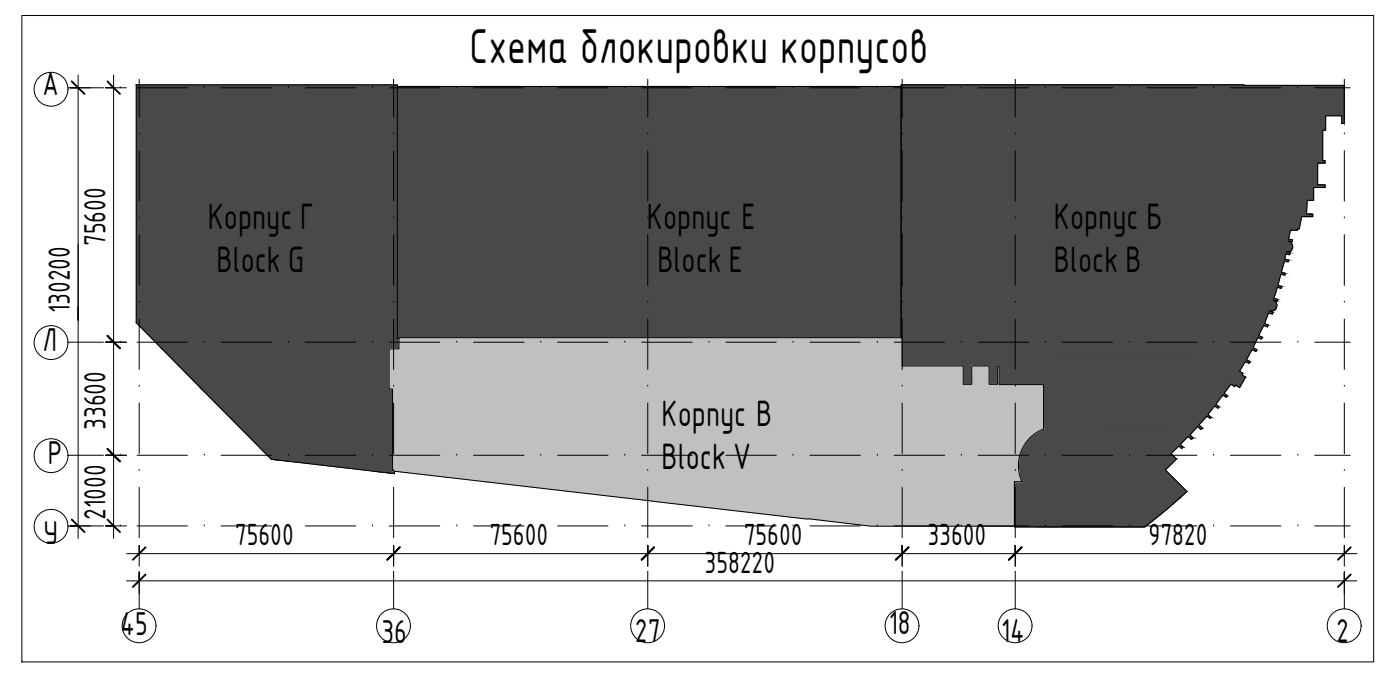

1. Лист смотреть совместно с л. 7-11.
2. Схемы дверных блоков и спецификацию элементов заполнения проемов смотреть на л. 12.
3. Ведомость отделки помещений смотреть на л. 37.
4. План полов смотреть на листе 26, 26.1, 26.2, 26.3, 26.4. Экспликация полов дана на л. 27.
5. Стояки и воздуховоды зашить по месту. Расход материала смотри в в спецификацию расхода материалов на л. 24 настоящего альбома.
6. Против ревизий на стояках канализации в коробах зашивки предусмотреть по месту установку нажимных люков под плитку размером 300х400h на высоте 800 мм от чистого пола в помещениях с отделкой стен плиткой; декоративных нажимных люков в помещениях со стенами под покраску.
7. Коммуникации, зашитые ГКЛ и кирпичной кладкой, оборудовать лючками с нажимным механизмом, согласно пункта 6. Замком борудовать двери для входа в ниши коммуникаций.
8. Направляющие ЗД-1 смотри раздел: Строительное задание Корпус В от "Гарантэнерго" Шифр: 5КС-АТК-С3.
9. Ведомость окраски стен помещний автостоянки см. л. 37.
10. Выполнить затирку цементно-песчаным раствором до достижения ровной гладкой поверхности, как по горизонтали, так и по вертикали с последующим нанесением одного слоя шпатлевки.
11. Расстановку машиномест их привязки, узел устройства колесоотбойников и их точное размещение см. СБД-КУТ03-КМП-2-25-Р-100-ТХ.01.00. Технологические решения. Подземная автостоянка.
12. Корректировка данного листа выполнена на основании исходных данных раздела АР. СБД-1276-ПК-КУТ03-0000-АР01.00, выполненной компанией ТПО "Прайд".
13. Маркировка и грузоподъемность лифтов указаны на основании Приложения №5 "Схема вертикального транспорта Корпуса В" к официальному письму от ООО "СБД" от 06.02.2024 № КУТ06-06_392 "О направлении требований к корректировке РД по -1, -2, -3, -4, -5 эт."
14. Устройство ЭнергоЦентра см. л. 55.4-55.8

С выпуском данного листа аннулировать лист №3 Прайдекс Констракшн шифр PR-200.СБВ.АР01.00 (изм.3. 12.23).

0,000 = 147,500

Согласовано
Взам. инв. №
Подп. и дата
Инв. № подл.

| | | | | | | |
|---|---|---|---|---|---|---|
| 1 | | Изм. | 3932/26 | | 06.26 | |
| Изм. | Кол уч. | Лист | № док. | Подпись | Дата | |
| Разработал | | Бугакова | | | 24.03.26 | |
| Проверил | | Бугакова | | | 24.03.26 | |
| ГАП | | Пичурова | | | 24.03.26 | |
| ГИП | | Хорлуков | | | 24.03.26 | |
| Н.контроль | | Пичурова | | | 24.03.26 | |

КУТ03-Р-ПИР-2-26-100 - АР01.01.00

Реконструкция делового комплекса в составе корп. «А», «Б», «В», «Г», «Е» с единой стилобатной подземной частью и устройством надземной объединительной аркады по адресу: пересечение Кутузовского проспекта и улицы Кульнева, район Дорогомилово, Западный административный округ города Москвы

Архитектурные решения. Подземная автостоянка (Стилобат)

| Стадия | Лист | Листов |
|---|---|---|
| Р | 5 | |

План -2 этажа на отметке -8,100

MARKS ENGINEERING

Формат А2х3