План -2 этажа
М 1:200

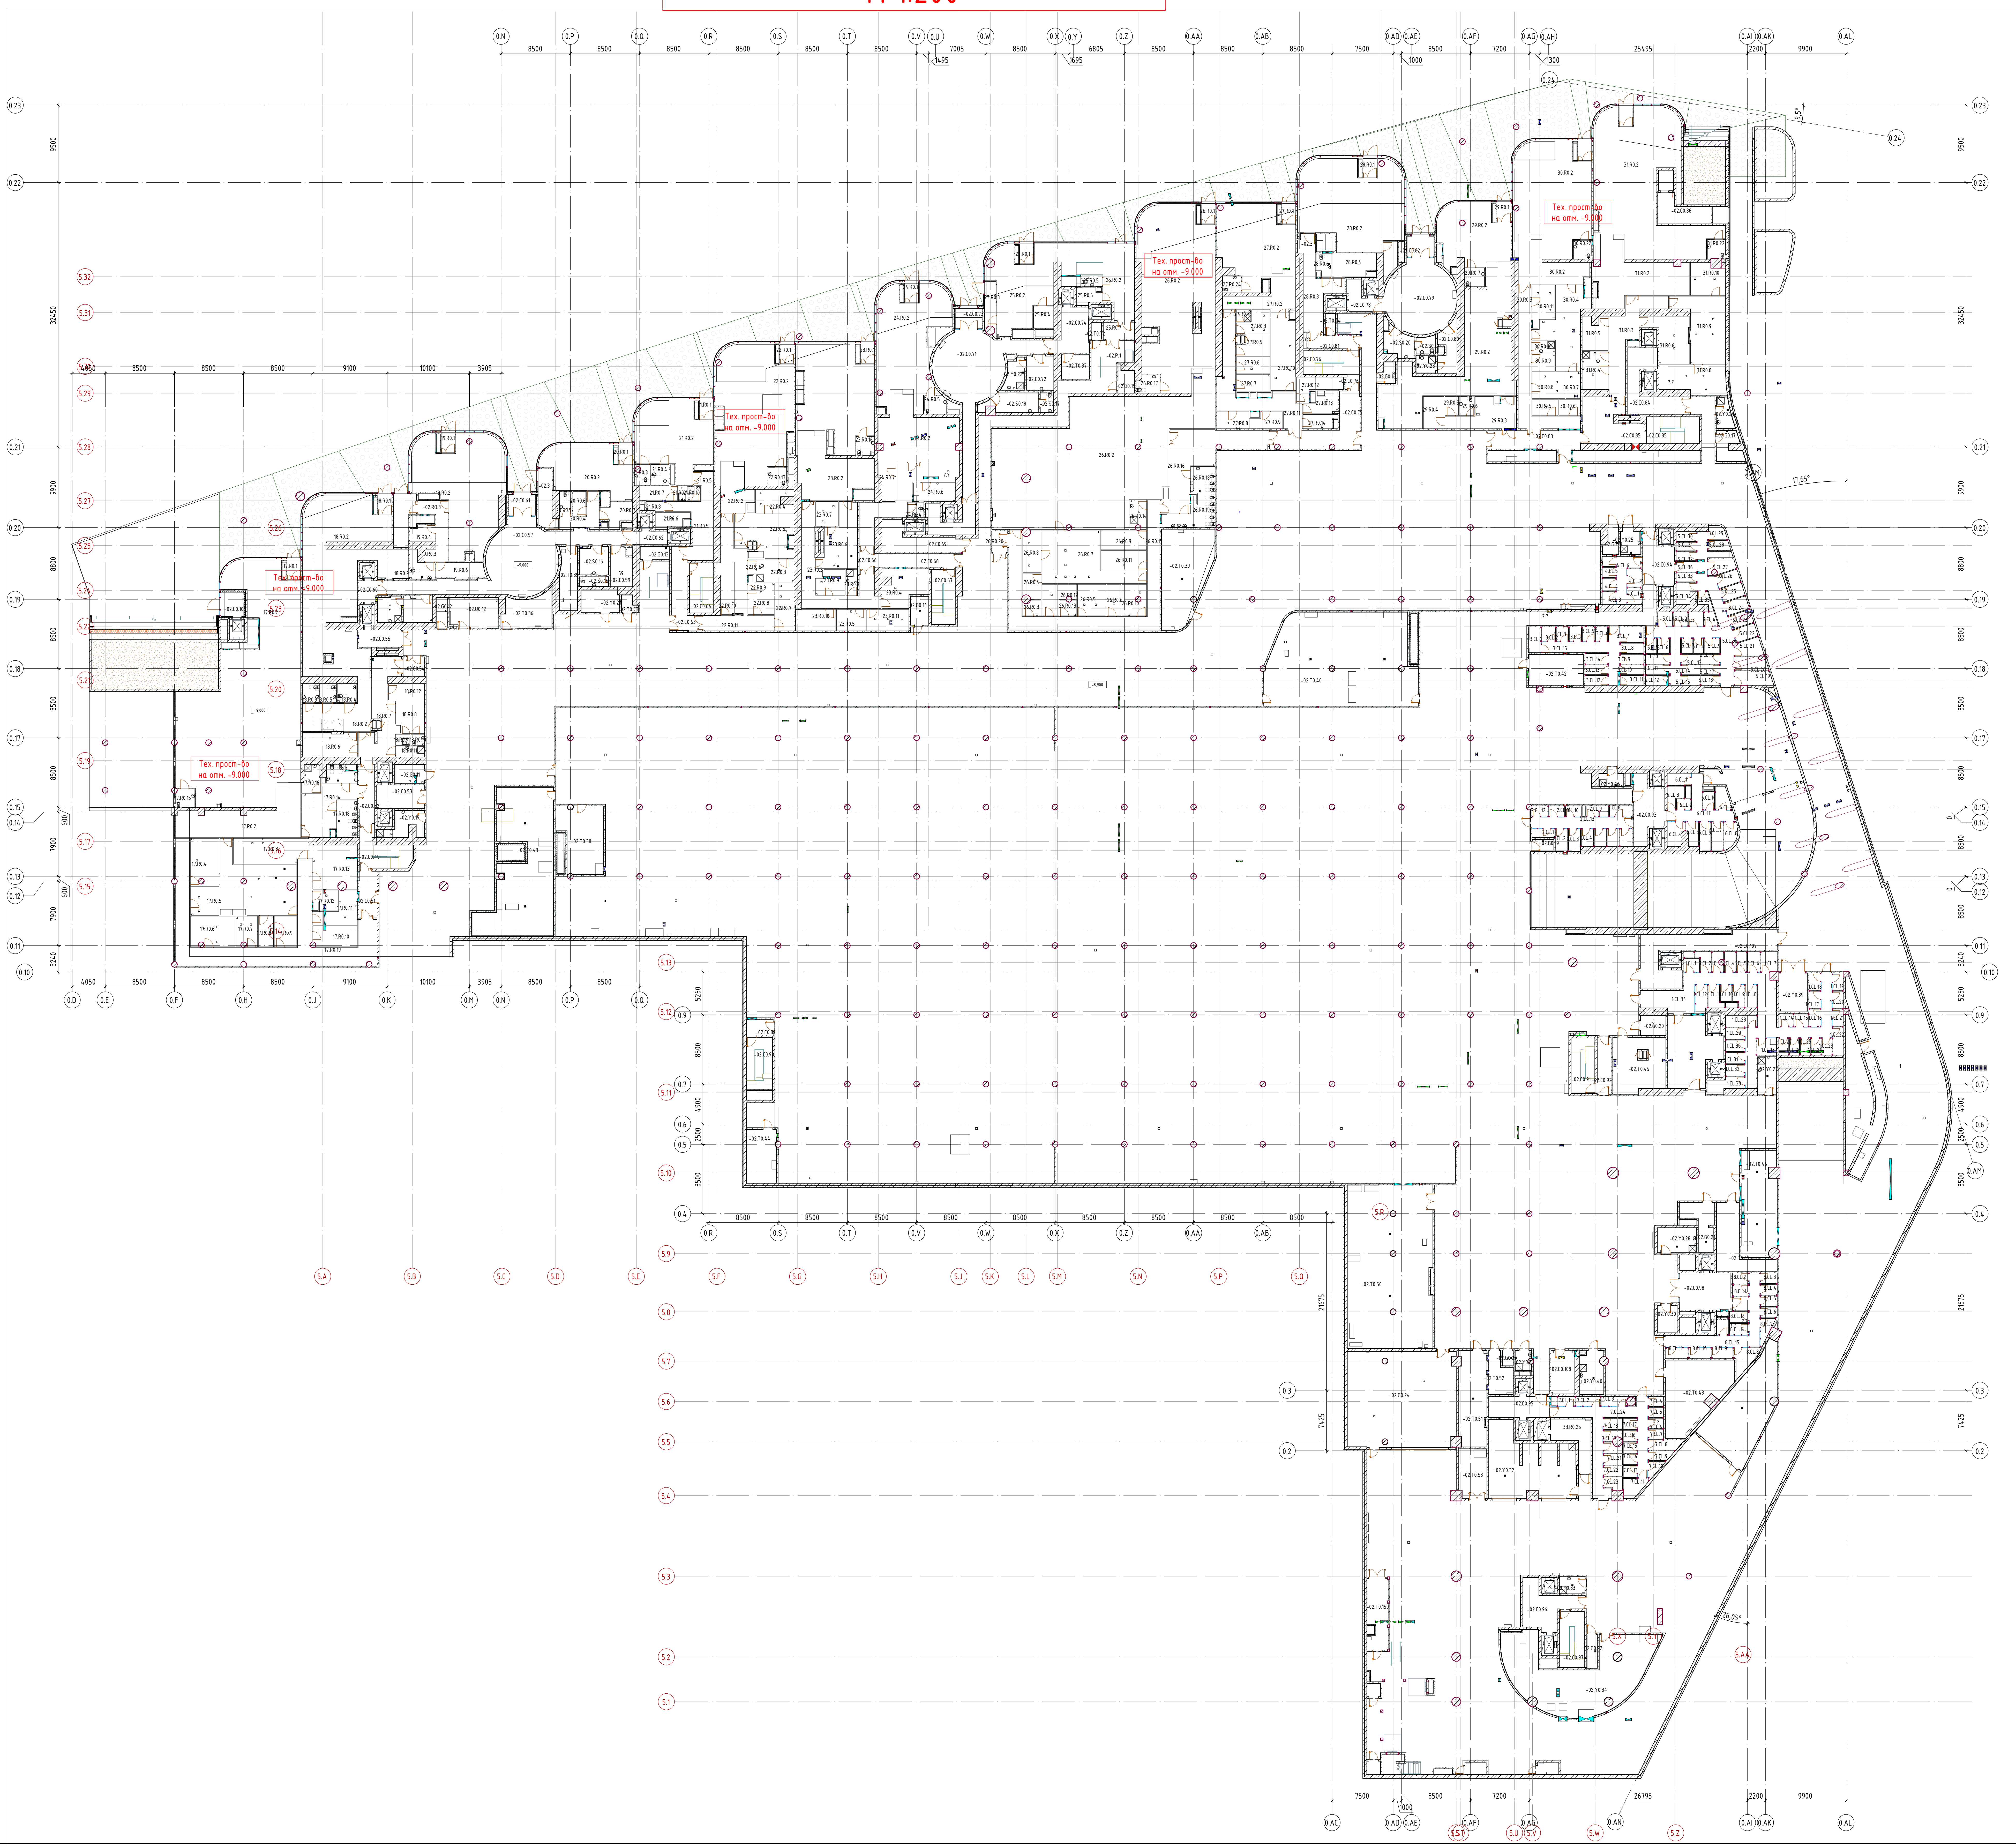
Тех. прост-во на отм. -9.000
Тех. прост-во на отм. -9.000
Тех. прост-во на отм. -9.000
Тех. прост-во на отм. -9.000
Тех. прост-во на отм. -9.000
17,65°
13,5°
29,05°

Экспликация помещений -2 этажа

№ пом.	Наименование	Площадь, м²	Кат. пом.
Блок кладовых под аренду -02.CL.1			
1.CL.1	Кладовая под аренду	3,30	В2
1.CL.2	Кладовая под аренду	4,00	В2
1.CL.3	Кладовая под аренду	3,30	В2
1.CL.4	Кладовая под аренду	3,70	В2
1.CL.5	Кладовая под аренду	3,20	В2
1.CL.6	Кладовая под аренду	4,00	В2
1.CL.7	Кладовая под аренду	5,00	В2
1.CL.8	Кладовая под аренду	4,30	В2
1.CL.9	Кладовая под аренду	3,50	В2
1.CL.10	Кладовая под аренду	3,00	В2
1.CL.11	Кладовая под аренду	4,60	В2
1.CL.12	Кладовая под аренду	5,40	В2
1.CL.13	Кладовая под аренду	5,10	В2
1.CL.14	Кладовая под аренду	2,90	В2
1.CL.15	Кладовая под аренду	2,90	В2
1.CL.16	Кладовая под аренду	3,30	В2
1.CL.17	Кладовая под аренду	3,10	В2
1.CL.18	Кладовая под аренду	3,20	В2
1.CL.19	Кладовая под аренду	3,00	В2
1.CL.20	Кладовая под аренду	2,90	В2
1.CL.21	Кладовая под аренду	2,90	В2
1.CL.22	Кладовая под аренду	4,50	В2
1.CL.23	Кладовая под аренду	2,70	В2
1.CL.24	Кладовая под аренду	2,60	В2
1.CL.25	Кладовая под аренду	2,60	В2
1.CL.26	Кладовая под аренду	2,60	В2
1.CL.27	Кладовая под аренду	2,60	В2
1.CL.28	Кладовая под аренду	5,80	В2
1.CL.29	Кладовая под аренду	3,40	В2
1.CL.30	Кладовая под аренду	3,40	В2
1.CL.31	Кладовая под аренду	3,40	В2
1.CL.32	Кладовая под аренду	3,40	В2
1.CL.33	Кладовая под аренду	7,40	В2
1.CL.34	Проход	74,80	В2
		195,80	
Блок кладовых под аренду -02.CL.2			
2.CL.1	Кладовая	3,30	В2
2.CL.2	Кладовая	4,30	В2
2.CL.3	Кладовая	4,30	В2
2.CL.4	Кладовая	3,40	В2
2.CL.5	Кладовая	3,40	В2
2.CL.6	Кладовая	3,40	В2
2.CL.7	Кладовая	3,40	В2
2.CL.8	Кладовая	3,90	В2
2.CL.9	Кладовая	3,00	В2
2.CL.10	Кладовая	2,70	В2
2.CL.11	Кладовая	2,70	В2
2.CL.12	Кладовая	2,70	В2
2.CL.13	Проход	16,20	В2
		56,70	
Блок кладовых под аренду -02.CL.3			
3.CL.1	Кладовая под аренду	5,00	В2
3.CL.2	Кладовая под аренду	3,10	В2
3.CL.3	Кладовая под аренду	2,80	В2
3.CL.4	Кладовая под аренду	2,80	В2
3.CL.5	Кладовая под аренду	2,80	В2
3.CL.6	Кладовая под аренду	2,70	В2
3.CL.7	Кладовая под аренду	5,70	В2
3.CL.8	Кладовая под аренду	3,80	В2
3.CL.9	Кладовая под аренду	3,60	В2
3.CL.10	Кладовая под аренду	3,60	В2
3.CL.11	Кладовая под аренду	3,60	В2
3.CL.12	Кладовая под аренду	3,50	В2
3.CL.13	Кладовая под аренду	3,50	В2
3.CL.14	Кладовая под аренду	3,80	В2
3.CL.15	Проход	20,30	В2
		70,60	
Блок кладовых под аренду -02.CL.4			
4.CL.1	Кладовая под аренду	3,60	В2
4.CL.2	Кладовая под аренду	4,00	В2
4.CL.3	Кладовая под аренду	2,80	В2
4.CL.4	Кладовая под аренду	2,80	В2
4.CL.5	Кладовая под аренду	2,20	В2
4.CL.6	Проход	9,70	В2
4.CL.7	Кладовая под аренду	2,20	В2
		27,30	
Блок кладовых под аренду -02.CL.5			
5.CL.1	Кладовая под аренду	3,30	В2
5.CL.2	Кладовая под аренду	3,30	В2
5.CL.3	Кладовая под аренду	3,30	В2
5.CL.4	Кладовая под аренду	2,80	В2
5.CL.5	Кладовая под аренду	2,70	В2
5.CL.6	Кладовая под аренду	2,90	В2
5.CL.7	Кладовая под аренду	2,80	В2
5.CL.8	Кладовая под аренду	2,40	В2
5.CL.9	Кладовая под аренду	3,70	В2
5.CL.10	Кладовая под аренду	3,70	В2
5.CL.11	Кладовая под аренду	3,70	В2
5.CL.12	Кладовая под аренду	3,70	В2
5.CL.13	Кладовая под аренду	2,90	В2
5.CL.14	Кладовая под аренду	2,90	В2
5.CL.15	Кладовая под аренду	2,90	В2
5.CL.16	Кладовая под аренду	2,90	В2
5.CL.17	Кладовая под аренду	2,90	В2
5.CL.18	Кладовая под аренду	2,90	В2
5.CL.19	Кладовая под аренду	8,20	В2
5.CL.20	Кладовая под аренду	6,70	В2
5.CL.21	Кладовая под аренду	6,50	В2
5.CL.22	Кладовая под аренду	4,70	В2
5.CL.23	Кладовая под аренду	4,70	В2
5.CL.24	Кладовая под аренду	4,70	В2
5.CL.25	Кладовая под аренду	4,70	В2
5.CL.26	Кладовая под аренду	4,60	В2
5.CL.27	Кладовая под аренду	5,50	В2
5.CL.28	Кладовая под аренду	3,20	В2
5.CL.29	Кладовая под аренду	3,80	В2
5.CL.30	Кладовая под аренду	3,30	В2
5.CL.31	Кладовая под аренду	2,70	В2
5.CL.32	Кладовая под аренду	2,90	В2
5.CL.33	Кладовая под аренду	2,90	В2
5.CL.34	Кладовая под аренду	5,50	В2
5.CL.35	Кладовая под аренду	2,90	В2
5.CL.36	Проход	51,10	В2
		184,30	
Блок кладовых -02.CL.6			
6.CL.1	Кладовая под аренду	4,50	В2
6.CL.2	Кладовая под аренду	2,50	В2
6.CL.3	Кладовая под аренду	4,70	В2
6.CL.4	Кладовая под аренду	5,90	В2
6.CL.5	Кладовая под аренду	4,30	В2
6.CL.6	Кладовая под аренду	5,20	В2
6.CL.7	Кладовая под аренду	5,20	В2
6.CL.8	Кладовая под аренду	5,00	В2
6.CL.9	Кладовая под аренду	5,00	В2
6.CL.10	Кладовая под аренду	3,20	В2
6.CL.11	Проход	16,80	В2
		62,30	

Экспликация помещений -2 этажа

№ пом.	Наименование	Площадь, м²	Кат. пом.
Блок кладовых -02.CL.7			
7.CL.1	Кладовая	2,70	В2
7.CL.2	Кладовая	3,90	В2
7.CL.3	Кладовая	4,30	В2
7.CL.4	Кладовая	2,30	В2
7.CL.5	Кладовая	2,30	В2
7.CL.6	Кладовая	2,30	В2
7.CL.7	Кладовая	2,30	В2
7.CL.8	Кладовая	4,90	В2
7.CL.9	Кладовая	3,30	В2
7.CL.10	Кладовая	2,80	В2
7.CL.11	Кладовая	5,90	В2
7.CL.13	Кладовая	2,70	В2
7.CL.14	Кладовая	2,30	В2
7.CL.15	Кладовая	2,40	В2
7.CL.16	Кладовая	2,40	В2
7.CL.17	Кладовая	2,40	В2
7.CL.18	Кладовая	3,30	В2
7.CL.19	Кладовая	2,80	В2
7.CL.20	Кладовая	2,80	В2
7.CL.21	Кладовая	3,30	В2
7.CL.22	Кладовая	3,10	В2
7.CL.23	Кладовая	3,50	В2
7.CL.24	Проход	40,80	В2
		108,80	
Блок кладовых -02.CL.8			
8.CL.1	Кладовая	2,90	В2
8.CL.2	Кладовая	2,90	В2
8.CL.3	Кладовая	2,80	В2
8.CL.4	Кладовая	2,80	В2
8.CL.5	Кладовая	2,80	В2
8.CL.6	Кладовая	2,80	В2
8.CL.7	Кладовая	3,90	В2
8.CL.8	Кладовая	7,40	В2
8.CL.9	Кладовая	3,60	В2
8.CL.10	Кладовая	3,80	В2
8.CL.11	Кладовая	3,90	В2
8.CL.12	Кладовая	3,30	В2
8.CL.13	Кладовая	3,30	В2
8.CL.14	Кладовая	3,60	В2
8.CL.15	Проход	29,60	В2
		79,40	
Предприятия общественного питания №11			
17.R0.1	Тамбур	4,40	
17.R0.2	Обеденный зал	377,80	
17.R0.3	Моечная столовой посуды	27,70	Д
17.R0.4	Холодный цех	20,20	В4
17.R0.5	Горячий цех	71,70	В3
17.R0.6	Холодильные камеры	20,10	В3
17.R0.7	Овощной цех	9,60	В4
17.R0.8	Моечная кухонной посуды	7,00	Д
17.R0.9	Мясо-рыбный цех	10,30	В3
17.R0.10	Помещение загрузки	13,70	В4
17.R0.11	Кладовая и моечная тары	15,10	В4
17.R0.12	Камера пищевых отходов	7,00	В4
17.R0.13	Кладовая сухих продуктов	29,70	В3
17.R0.14	Коридор	29,10	
17.R0.15	Универсальный санузел МГН	5,40	
17.R0.16	ПУИ (предприятие питания)	7,20	В4
17.R0.17	Санузел муж.	7,30	
17.R0.18	Санузел жен.	11,70	
17.R0.19	Коридор	106,40	
		781,40	
Предприятие общественного питания №12			
18.R0.1	Тамбур	4,40	
18.R0.2	Обеденный зал	314,10	
18.R0.3	Санузел муж.	4,70	
18.R0.4	Универсальный санузел МГН	5,60	
18.R0.5	Санузел жен.	4,80	
18.R0.6	Помещение подготовки продуктов к реализации	19,10	В3
18.R0.7	Коридор	37,10	
18.R0.8	Раздевалка персонала	13,30	
18.R0.9	Душевая персонала	2,40	
18.R0.10	Санузел персонала	2,30	
18.R0.11	ПУИ (предприятие питания)	4,70	В4
18.R0.12	Помещение загрузки	8,90	В4
		421,40	
Предприятие торговли №7			
19.R0.1	Тамбур	4,40	
19.R0.2	Торговый зал	122,60	
19.R0.3	Коридор	17,10	
19.R0.4	Помещение приемки товаров	6,10	В4
19.R0.5	Санузел персонала с местом УИ	7,90	
19.R0.6	Подсобное помещение	11,20	В3
		169,30	
Предприятие торговли №8			
20.R0.1	Тамбур	4,40	
20.R0.2	Торговый зал	56,70	
20.R0.3	Тамбур	13,50	
20.R0.4	Коридор	11,90	
20.R0.5	Санузел персонала с местом УИ	4,70	
20.R0.6	Помещение приемки товаров	4,90	В4
20.R0.7	Подсобное помещение	9,70	В3
		105,80	
Предприятие общественного питания №13			
21.R0.1	Тамбур	4,40	
21.R0.2	Обеденный зал	75,20	
21.R0.3	Санузел	4,50	
21.R0.4	Универсальный санузел МГН	5,70	
21.R0.5	Коридор	30,70	
21.R0.6	Помещение подготовки продуктов к реализации	6,40	В4
21.R0.7	Раздевалка персонала	8,20	
21.R0.8	Санузел персонала	2,60	
21.R0.9	Душевая персонала	1,70	
21.R0.10	ПУИ (предприятие питания)	3,00	В4
		142,40	
Предприятия общественного питания №14			
22.R0.1	Тамбур	4,40	
22.R0.2	Обеденный зал	152,60	
22.R0.3	Моечная кухонной посуды	10,00	Д
22.R0.4	Моечная столовой посуды	12,20	Д
22.R0.5	Доготовочный цех	32,40	В3
22.R0.6	ПУИ (предприятие питания)	4,80	В4
22.R0.7	Холодильная камера	13,70	В3
22.R0.8	Кладовая сухих продуктов	7,40	В4
22.R0.9	Кладовая и моечная тары	4,80	В4
22.R0.10	Помещение приемки	10,30	В4
22.R0.11	Коридор	38,50	
22.R0.13	Санузел для МГН	5,30	
		296,40	

Экспликация помещений -2 этажа

№ пом.	Наименование	Площадь, м²	Кат. пом.
Предприятия общественного питания №15			
23.R0.1	Тамбур	4,40	
23.R0.2	Обеденный зал	150,60	
23.R0.3	Коридор	39,80	
23.R0.4	Помещение загрузки	22,80	В3
23.R0.5	Кладовая и моечная тары	9,50	В4
23.R0.6	Доготовочный цех	29,30	В3
23.R0.7	Моечная столовой посуды	8,50	Д
23.R0.8	ПУИ (предприятие питания)	4,50	В4
23.R0.9	Моечная кухонной посуды	10,40	Д
23.R0.10	Кладовая сухих продуктов	13,00	В3
23.R0.11	Холодильная камера	13,70	В3
23.R0.16	Санузел для МГН	5,00	
		311,50	
Предприятие торговли №9			
24.R0.1	Тамбур	4,40	
24.R0.2	Торговый зал	157,90	
24.R0.3	Коридор	40,30	
24.R0.4	Санузел персонала с местом УИ	3,40	
24.R0.5	Универсальный санузел МГН	6,10	
24.R0.6	Подсобное помещение	10,10	В3
24.R0.7	Помещение приемки товаров	8,60	В4
		230,80	
Предприятие торговли №10			
25.R0.1	Тамбур	4,40	
25.R0.2	Торговый зал	112,10	
25.R0.3	Тамбур	8,40	
25.R0.4	Подсобное помещение	6,80	В4
25.R0.5	Санузел персонала с местом УИ	3,20	
25.R0.6	Помещение приемки товаров	5,20	В4
25.R0.7	Переход (тамбур-шлюз)	7,90	
		148,00	
Предприятия общественного питания №16			
26.R0.1	Тамбур	4,40	
26.R0.2	Обеденный зал	504,80	
26.R0.3	Помещение загрузки	4,00	В4
26.R0.4	Моечная кухонной посуды	6,80	Д
26.R0.5	Холодильные камеры	13,50	В3
26.R0.6	Кладовая и моечная тары	6,70	В4
26.R0.7	Горячий цех	55,80	В3
26.R0.8	Моечная столовой посуды	11,00	Д
26.R0.9	Холодный цех	13,40	В3
26.R0.10	Мясо-рыбный цех	11,20	В4
26.R0.11	Овощной цех	13,40	В3
26.R0.12	Кладовая сухих продуктов	12,00	В3
26.R0.13	Камера пищевых отходов	3,80	В4
26.R0.14	ПУИ (предприятие питания)	7,00	В4
26.R0.15	Коридор	71,60	
26.R0.16	Коридор	55,30	
26.R0.18	Санузел муж.	9,80	
26.R0.19	Санузел жен.	15,70	
26.R0.20	Переход (тамбур-шлюз)	5,00	
		825,20	
Предприятия общественного питания №17			
26.R0.17	Санузел для МГН	6,10	
		6,10	
Предприятия общественного питания №17			
27.R0.1	Тамбур	4,40	
27.R0.2	Обеденный зал	99,60	
27.R0.3	Моечная столовой посуды	9,20	Д
27.R0.4	ПУИ (предприятие питания)	2,80	В4
27.R0.5	Холодный цех	9,40	В4
27.R0.6	Овощной цех	8,50	В4
27.R0.7	Мясо-рыбный цех	8,50	В4
27.R0.8	Холодильная камера	8,30	В4
27.R0.9	Кладовая сухих продуктов	7,30	В4
27.R0.10	Горячий цех	27,10	В3
27.R0.11	Коридор	42,50	
27.R0.12	Моечная кухонной посуды	11,30	Д
27.R0.13	Помещение загрузки	8,40	В4
27.R0.14	Кладовая и моечная тары	6,50	В4
27.R0.24	Санузел для МГН	4,80	
		258,60	
Предприятие торговли №11			
28.R0.1	Тамбур	4,40	
28.R0.2	Торговый зал	128,20	
28.R0.3	Коридор	31,20	
28.R0.4	Помещение приёмки товаров	15,30	В4
28.R0.5	Подсобное помещение	6,80	
28.R0.6	Санузел персонала с местом УИ	5,00	
		190,90	
Предприятие торговли №12			
29.R0.1	Тамбур	4,40	
29.R0.2	Торговый зал	184,60	
29.R0.3	Коридор	24,90	
29.R0.4	Подсобное помещение	10,00	В3
29.R0.5	Помещение приемки товаров	3,90	В4
29.R0.6	Санузел персонала с местом УИ	4,30	
29.R0.7	Универсальный санузел МГН	5,70	
		237,80	
Предприятие общественного питания №18			
30.R0.1	Тамбур	4,60	
30.R0.2	Обеденный зал	146,30	
30.R0.3	Коридор	37,60	
30.R0.4	Доготовочный цех	41,00	В3
30.R0.5	Кладовая и моечная тары	6,30	Д
30.R0.6	Помещение загрузки	5,20	В4
30.R0.7	Моечная кухонной посуды	5,80	Д
30.R0.8	Холодильная камера	13,20	В3
30.R0.9	Кладовая сухих продуктов	6,00	В4
30.R0.10	ПУИ (предприятие питания)	4,10	В4
30.R0.11	Моечная столовой посуды	11,70	Д
30.R0.22	Универсальный санузел МГН	5,20	
		287,00	
Предприятия общественного питания №19			
31.R0.1	Тамбур	4,30	
31.R0.2	Обеденный зал	238,10	
31.R0.3	Коридор	32,60	
31.R0.4	Помещение загрузки	10,10	В4
31.R0.5	Кладовая сухих продуктов	12,40	В3
31.R0.6	Холодильная камера	25,30	В3
31.R0.7	ПУИ (предприятие питания)	4,70	В4
31.R0.8	Моечная кухонной посуды	27,70	Д
31.R0.9	Доготовочный цех	40,10	В3
31.R0.10	Моечная столовой посуды	16,70	Д
31.R0.22	Универсальный санузел МГН	5,30	
		417,30	
Предприятие при танцевальных залах №21			
33.R0.25	Лифтовой холл (тамбур-шлюз)	19,20	
		19,20	

Экспликация помещений МОП -2 этажа

№ пом.	Номер	Наименование	Площадь, м²	Кат. пом.
МОП				
-02.C0.49	49	ЛК №0.8 (Н2)	18,50	
-02.C0.51	51	Коридор безопасности	12,70	
-02.C0.52	52	Коридор безопасности	13,80	
-02.C0.53	53	Лифтовой холл (тамбур-шлюз)	17,20	
-02.C0.54	54	Переход (тамбур-шлюз)	6,30	
-02.C0.55	55	Лифтовой холл (тамбур-шлюз)	11,10	
-02.C0.57	57	Вестибюль	109,90	
-02.C0.58	58	Колясочная	11,80	В3
-02.C0.59	59	Колясочная	12,40	В3
-02.C0.60	60	Лифтовой холл (тамбур-шлюз)	5,70	
-02.C0.61	61	Тамбур	9,30	
-02.C0.62	62	Лифтовой холл (тамбур-шлюз)	5,60	
-02.C0.63	63	Коридор безопасности	23,50	
-02.C0.64	64	ЛК №0.9 (Н2)	17,70	
-02.C0.66	66	Коридор безопасности	22,50	
-02.C0.67	67	ЛК №0.10 (Н2)	19,40	
-02.C0.69	69	Лифтовой холл (тамбур-шлюз)	23,00	
-02.C0.70	70	Лифтовой холл (тамбур-шлюз)	16,90	
-02.C0.71	71	Вестибюль	94,60	
-02.C0.72	72	Колясочная	14,30	В3
-02.C0.73	73	Тамбур	8,90	
-02.C0.74	74	Лифтовой холл (тамбур-шлюз)	19,20	
-02.C0.75	75	Коридор безопасности	36,90	
-02.C0.76	76	ЛК №0.11 (Н2)	22,50	
-02.C0.78	78	Лифтовой холл (тамбур-шлюз)	10,20	
-02.C0.79	79	Вестибюль	65,90	
-02.C0.80	80	Колясочная	12,60	В3
-02.C0.81	81	Переход (тамбур-шлюз)	10,40	
-02.C0.82	82	Тамбур	8,40	
-02.C0.83	83	Коридор безопасности	28,20	
-02.C0.84	84	Лифтовой холл (тамбур-шлюз)	30,80	
-02.C0.85	85	ЛК №0.12 (Н2)	54,80	
-02.C0.86	86	Тамбур (не отапливаемый)	21,40	
-02.C0.89	89	Переход (тамбур-шлюз)	6,30	
-02.C0.90	90	ЛК №0.1.2 (Н3)	24,20	
-02.C0.91	91	ЛК №0.1.3 (Н3)	19,30	
-02.C0.92	92	Переход (тамбур-шлюз)	11,90	
-02.C0.93	93	Лифтовой холл (тамбур-шлюз)	24,70	
-02.C0.94	94	Лифтовой холл (тамбур-шлюз)	20,90	
-02.C0.95	95	Лифтовой холл (тамбур-шлюз)	19,30	
-02.C0.96	96	Лифтовой холл (тамбур-шлюз)	27,60	
-02.C0.97	97	ЛК №0.15 (Н3)	20,50	
-02.C0.98	98	Лифтовой холл (тамбур-шлюз)	28,50	
-02.C0.99	99	Лифтовой холл (тамбур-шлюз)	48,20	
-02.C0.106	106	Тамбур	8,70	
-02.C0.107	107	Лифтовой холл (тамбур-шлюз)	58,00	
-02.C0.108	108	Колясочная	16,00	В3
			1130,50	
Подземная автостоянка				
-02.P.1	1	Помещение для хранения автомобилей	4961,00	В2
-02.P.4	4	Помещение для хранения автомобилей	7821,20	В2
			12782,20	
Сбор мусора				
-02.G0.11	11	Помещение ТБО	8,10	В4
-02.G0.12	12	Помещение ТБО	5,00	В4
-02.G0.13	13	Помещение ТБО	5,50	В4
-02.G0.14	14	Помещение ТБО	7,70	В4
-02.G0.15	15	Помещение ТБО	5,70	В4
-02.G0.16	16	Помещение ТБО	4,50	В4
-02.G0.17	17	Помещение ТБО	9,70	В4
-02.G0.18	18	Помещение ТБО	4,40	В4
-02.G0.19	19	Помещение ТБО	3,80	В4

Экспликация помещений МОП -2 этажа

№ пом.	Номер	Наименование	Площадь, м²	Кат. пом.
-02.G0.20	20	Помещение ТБО	7,60	В4
-02.G0.21	21	Помещение ТБО	15,60	В3
-02.G0.22	22	Помещение ТБО	5,00	В4
-02.G0.23	23	Помещение ТБО	2,40	В4
-02.G0.24	24	Мусоросборная камера(помещение компакторов ТБО)	154,50	В2
-02.G0.25	25	Помещение сбора КГО	74,30	В3
			313,80	
Служебные помещения				
-02.S0.15	15	Санузел персонала	4,10	
-02.S0.16	16	Помещение персонала	12,10	
-02.S0.17	17	Санузел персонала	4,00	
-02.S0.18	18	Помещение персонала	14,90	
-02.S0.19	19	Санузел персонала	5,00	
-02.S0.20	20	Помещение персонала	10,70	
			50,80	
Технические помещения				
-02.T0.35	35	Венткамера (вестибюль ДУ)	16,70	Д
-02.T0.36	36	Помещение СС	22,80	В3
-02.T0.37	37	Венткамера (вестибюль ДУ)	10,00	Д
-02.T0.38	38	Венткамера (автостоянка В Секция 5,9)	42,10	В2
-02.T0.39	39	Венткамера (торговые помещения В 3 этап)	63,70	Д
-02.T0.40	40	Венткамера (автостоянка П, КДУ Секция 7)	199,50	В2
-02.T0.42	42	Электрощитовая жилья	25,10	В2
-02.T0.43	43	Венткамера (автостоянка ДУ Секция 5,9)	129,20	В2
-02.T0.44	44	Электрощитовая автостоянки	24,00	В2
-02.T0.45	45	Электрощитовая автостоянки	41,00	В2
-02.T0.46	46	Венткамера (автостоянка В Секция 11)	54,80	В2
-02.T0.47	47	Электрощитовая жилья	29,90	В2
-02.T0.48	48	Электрощитовая офисов	58,80	В3
-02.T0.50	50	Венткамера	209,20	В2
-02.T0.51	51	Венткамера В	40,10	В2
-02.T0.52	52	Помещение СС	12,80	В3
-02.T0.53	53	Венткамера (автостоянка ДУ Секция 11)	20,80	В2
-02.T0.72	72	Помещение компрессорной гидравлических подъемников	2,50	В3
-02.T0.73	73	Помещение компрессорной гидравлических подъемников	3,40	В3
-02.T0.74	74	Помещение компрессорной гидравлических подъемников	3,10	В3
-02.T0.75	75	Помещение компрессорной гидравлических подъемников	2,60	В3
-02.T0.76	76	Помещение компрессорной гидравлических подъемников	2,60	В3
-02.T0.159	159	Помещение насосной станции для распределения реагентов	21,10	Д
			1035,80	
Уборка мест общего пользования				
-02.Y0.19	19	ПУИ (Жилая часть Секция 1)	12,40	В3
-02.Y0.20	20	ПУИ (Жилая часть Секция 2,3)	9,10	В4
-02.Y0.21	21	Склад инвентаря	12,50	В3
-02.Y0.22	22	ПУИ (Жилая часть Секция 4,5)	8,60	В3
-02.Y0.23	23	ПУИ (Жилая часть Секция 6)	5,00	В4
-02.Y0.24	24	ПУИ (Жилая часть Секция 7)	6,70	В4
-02.Y0.25	25	ПУИ (Жилая часть Секция 8)	6,90	В4
-02.Y0.26	26	ПУИ (Жилая часть Секция 9)	4,80	В4
-02.Y0.27	27	ПУИ (Жилая часть Секция 10)	10,20	В3
-02.Y0.28	28	ПУИ (Жилая часть Секция 11)	14,10	В3
-02.Y0.30	30	Помещение уборочной техники (автостоянка)	8,00	В4
-02.Y0.31	31	ПУИ (Жилая часть Секция 12)	4,50	В4
-02.Y0.32	32	Помещение внутренней техники	76,30	В2
-02.Y0.33	33	ПУИ (Жилая часть Секция 13)	6,30	В4
-02.Y0.34	34	Помещение внутренней техники	120,80	В3
-02.Y0.39	39	Помещение подметально-уборочной машины	16,30	В2
-02.Y0.40	40	ПУИ (автостоянка)	14,80	В3
			337,30	
Управляющая компания/Инженерная служба				
-02.U0.12	12	Кладовая ЗИП	21,70	В3
			21,70	

Условные обозначения:

🟩	-Помещения на отм. -3.650
🟪	-Помещения на отм. -3.950; -4.000
🟧	-Помещения на отм. -4.850
⬜	-Помещения на отм. -4.950; -5.000
🟪	-Помещения на отм. -5.380; -5.400; -5.440
🟧	-Помещения на отм. -5.850
🟦	-Помещения на отм. -7.000
🟩	-Помещения на отм. -8.800
▨	-Техническое прост-во на отм. -9.000
☐	-Помещения на отм. -12.770

Изм.	Кол.уч.	Лист	№ док.	Подпись	Дата

1042-Р-3 - ИСХ

«Многофункциональный жилой комплекс с подземной автостоянкой, апартаментами и встроенно-пристроенными нежилыми помещениями, с фрагментарной реставрацией и приспособлением объектов культурного наследия на территории Бадаевского пивоваренного завода, расположенного по адресу: Кутузовский проспект, вл. 12/2, 12/6, 12/3, 12/1, 12/4, 12/5, район Дорогомилово, Западный административный округ города Москвы»

Задания

Стадия	Лист	Листов
Р	5	

План -2-ого этажа

A0x2A

Согласовано
Взам. инв. №
Подп. и дата
Инв. № подл.