План -5 этажа на отметке -18,600
М 1 : 100

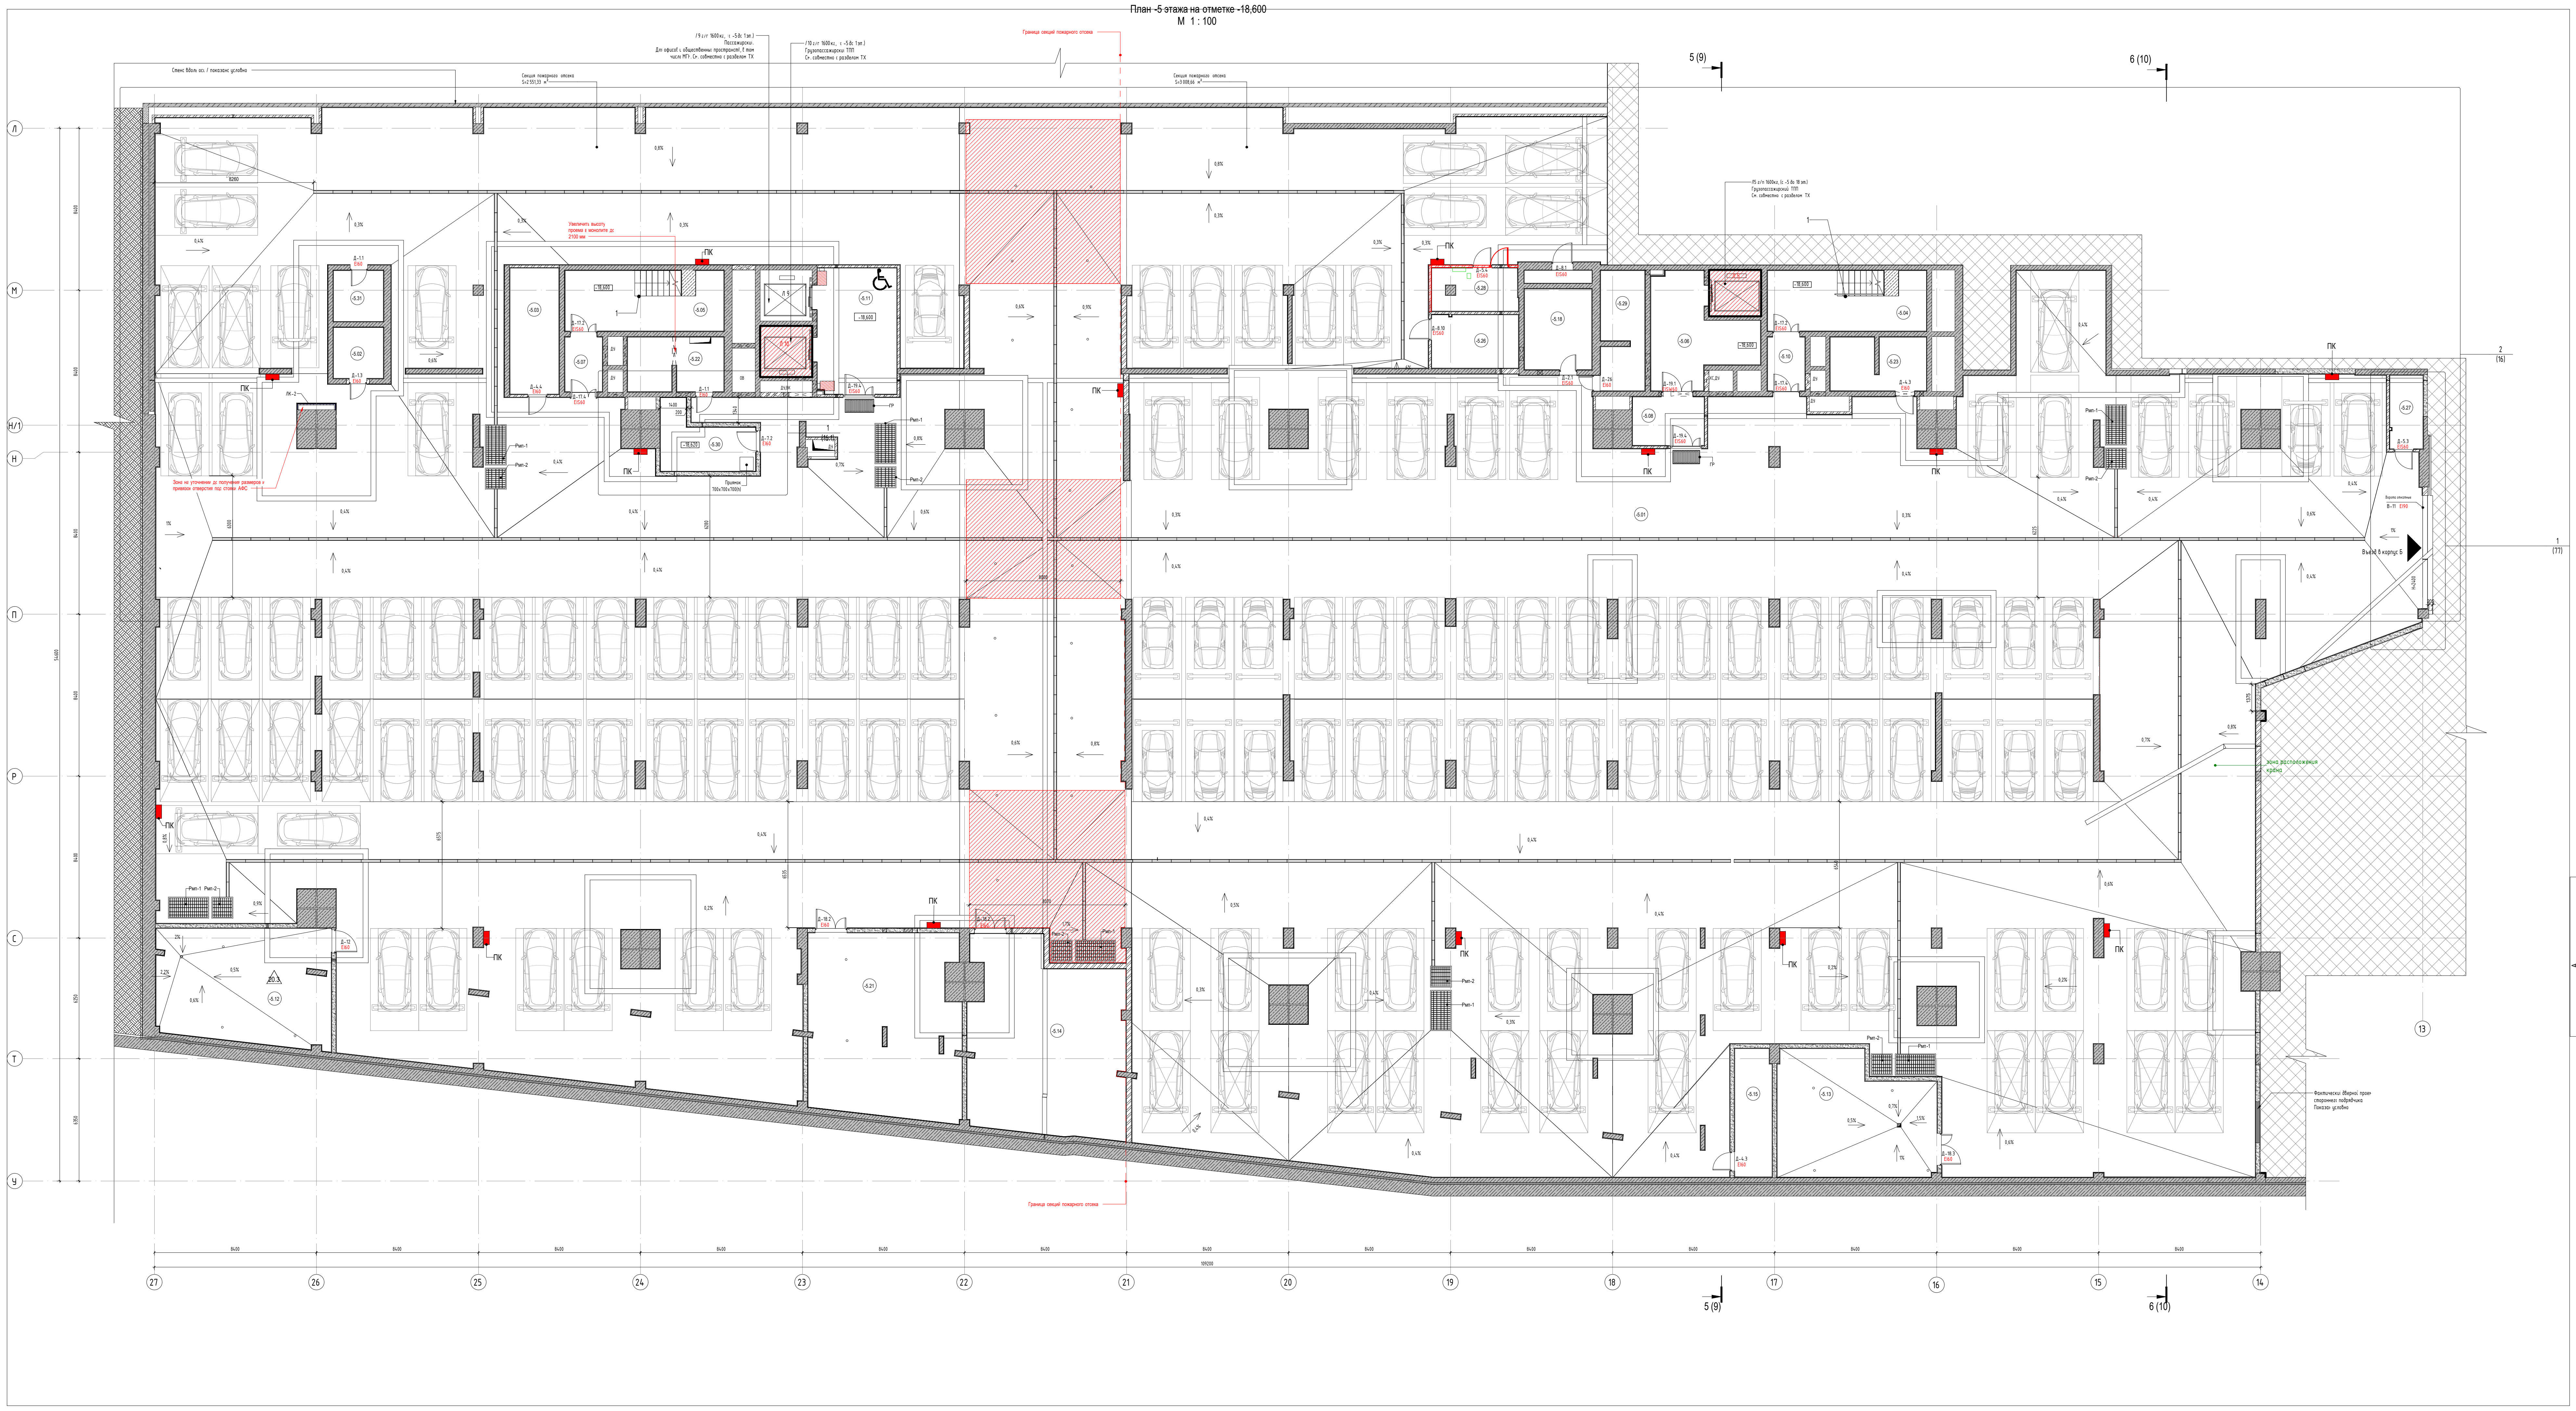
Граница секций пожарного отсека
Секция пожарного отсека S=3 008,66 м²
Секция пожарного отсека S=2 551,33 м²
Стена вдоль оси / показана условно
Л9 г/п 1600кг, (с -5 до 1эт.) Пассажирский. Для офисов и общественных пространств, в том числе МГН. См. совместно с разделом ТХ
Л10 г/п 1600кг, (с -5 до 1эт.) Грузопассажирский ТПП См. совместно с разделом ТХ
Л5 г/п 1600кг, (с -5 до 18 эт.) Грузопассажирский ТПП См. совместно с разделом ТХ
Увеличить высоту проема в монолите до 2100 мм
Ворота откатные В-11 EI90
Въезд в корпус Б
ПК
Рмп-1
Рмп-2
5 (9)
6 (10)
2 (16)
1 (77)
Л
М
М/1
Н
П
Р
С
Т
У
27
26
25
24
23
22
21
20
19
18
17
16
15
14

Экспликация помещений -5 этажа

Номер помещения	Наименование	Площадь, м²	Кат. пом.
01.Автостоянка			
-5.01	Помещение хранения автомобилей на 130 м/м	4765,33	В2
		4765,33	
14.Вспомогательные помещения			
-5.03	Помещение хранения пожарного инвентаря	16,82	В4
-5.29	Помещение хранения пожарного инвентаря	14,01	В4
-5.31	Помещение хранения пожарного инвентаря	6,96	В4
		37,79	
15.Места общего пользования			
-5.04	Лестничная клетка 2	26,00	
-5.05	Лестничная клетка 3	26,03	
-5.06	Лифтовый холл	23,24	
-5.07	Тамбур-шлюз	5,61	
-5.08	Тамбур-шлюз	9,78	
-5.10	Тамбур-шлюз	5,51	
-5.11	Лифтовый холл/ тамбур-шлюз	28,51	
		124,67	
16.Инженерные помещения			
-5.02	Помещение уборочной техники	6,94	В4
-5.12	Венткамера	53,18	Д
-5.13	Венткамера	48,93	Д
-5.14	Венткамера	75,57	В2
-5.15	Электрощитовая	12,97	В3
-5.18	Помещение фанкойла и газ.баллона	14,78	В3
-5.21	Венткамера	73,32	В3
-5.22	Электрощитовая	13,60	В3
-5.23	Электрощитовая	13,61	В3
-5.26	КУ АСО	12,62	В3
-5.27	Помещение вертикальных коммуникаций ИТ и СС	6,68	В4
-5.28	Помещение вертикальных коммуникаций ИТ и СС	9,83	В4
-5.30	Помещение КНС	12,35	Д
		354,38	
Итого		5282,17	

1.11

Ведомость машиномест -5 этаж

Наименование	Кол-во, шт.
Машино-место 5300х2500мм. Средний класс	96
Машино-место 5300х2500мм. Малый класс	14
Машино-место зависимое 5300х2500мм. Средний класс	21
	131

Условные обозначения:

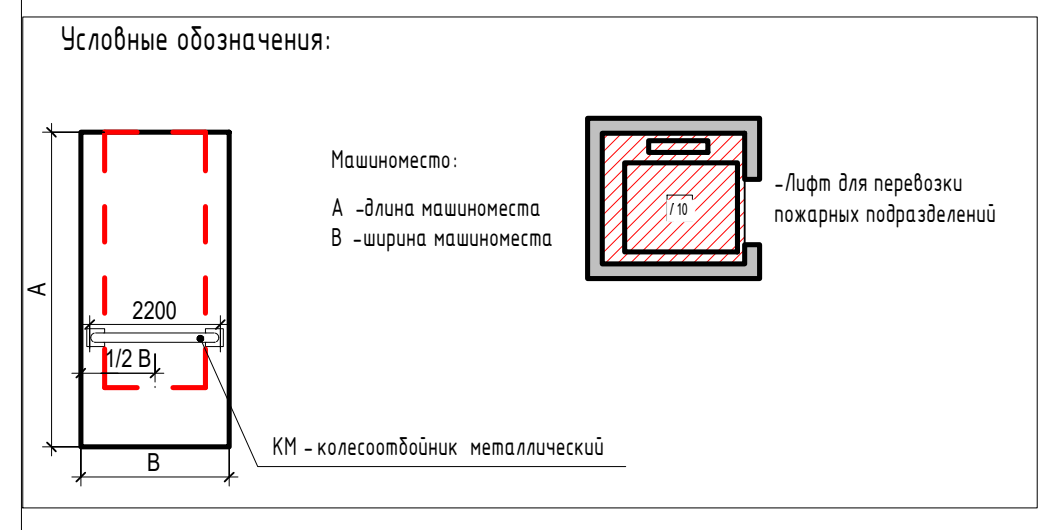

Машиноместо:

A -длина машиноместа
B -ширина машиноместа

КМ - колесоотбойник металлический

-Лифт для перевозки пожарных подразделений

Гр	- Грязезащитная решетка
1	- Тип лестничного ограждения
🟥	- Пожарный шкаф
← 0,3%	- Направление уклона пола
▨	Зона свободная от пожарной нагрузки

ПРИМЕЧАНИЯ

1. Лист смотреть совместно с л. 7-11.
2. Схемы дверных блоков и спецификацию элементов заполнения проемов смотреть на л.12.
3. Ведомость отделки помещений смотреть на л. 38.
4. План полов смотреть на л. 26, 26.1, 26.2, 26.3, 26.4. Экспликация полов дана на л. 27.
5. Стояки и воздуховоды зашить по месту. Расход материала смотри в спецификацию расхода материалов на л. 24 настоящего альбома.
6. Против ревизий на стояках канализации в коробах зашивки предусмотреть по месту установку нажимных люков под плитку размером 300х400h на высоте 800 мм от чистого пола в помещениях с отделкой стен плиткой; декоративных нажимных люков в помещениях со стенами под покраску.
7. Коммуникации, зашитые ГКЛ и кирпичной кладкой, оборудовать лючками с нажимным механизмом, согласно пункта 6. Замком борудовать двери для входа в ниши коммуникаций.
8. Направляющие ЗД-1 смотри раздел: Строительное задание Корпус В от "Гарантэнерго" Шифр: 5КС-АТК-С3.
9. Маркировка и привязка металлических колесоотбойников. Сведено в спецификацию расхода материалов на л. 24 настоящего альбома.
10. Ведомость окраски стен помещений автостоянки см. л. 38.
11. Выполнить затирку цементно-песчаным раствором до достижения ровной гладкой поверхности, как по горизонтали, так и по вертикали с последующим нанесением одного слоя шпатлевки.
12. Корректировка данного листа выполнена на основании исходных данных раздела АР
13. Шкафы управления на уточнении.
14. Маркировка и грузоподъемность лифтов указаны на основании Приложения №5 "Схема вертикального транспорта Корпуса В" к официальному письму от ООО "СБД" от 06.02.2024 № КУТ06-06_392 "О направлении требований к корректировке РД по -1, -2, -3, -4, -5 эт."
С выпуском данного листа аннулировать лист №2 ООО "Прайдекс Констракшн" шифр PR-200.СБВ.АР01.00 (изм.2, 09.23).
15. Расстановку машиномест их привязки, узел устройства колесоотбойников и их точное размещение см. СБД-КУТ03-КМП-2-25-Р-100-ТХ.01.00. Технологические решения. Подземная автостоянка.

Схема блокировки корпусов

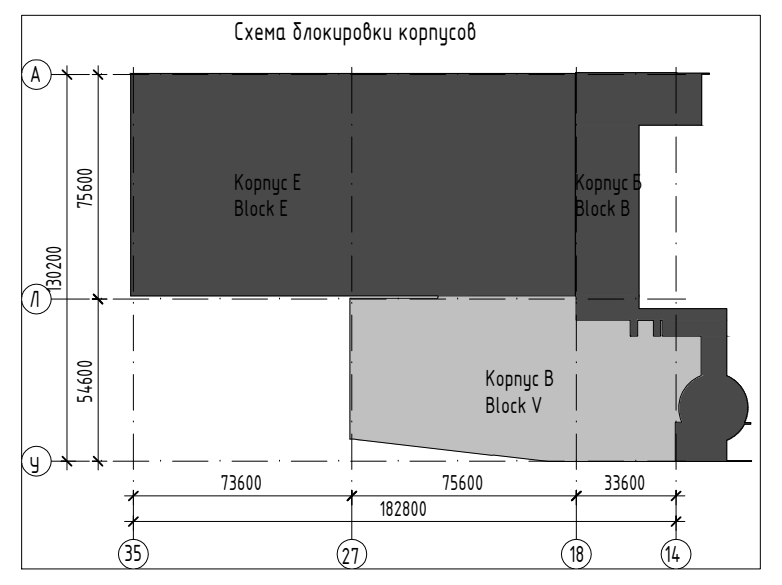

0,000 = 147,500

1		Изм.	3932/26		06.26	КУТ03-Р-ПИР-2-26-100 - АР01.01.00
Изм.	Кол уч.	Лист	№ док.	Подпись	Дата	Реконструкция делового комплекса в составе корп. «А», «Б», «В», «Г», «Е» с единой стилобатной подземной частью и устройством надземной объединительной аркады по адресу: пересечение Кутузовского проспекта и улиц Кульнева, район Дорогомилово, Западный административный округ города Москвы
Разработал	Дейчук				24.03.26	Архитектурные решения. Подземная автостоянка (Стилобат)
Проверил	Бугакова				24.03.26	Стадия: Р; Лист: 2; Листов:
ГАП	Пичурова				24.03.26	План -5 этажа на отметке -18,600
ГИП	Хорлуков				24.03.26	MARKS ENGINEERING
Н.контроль	Пичурова				24.03.26	

Формат А1x3