План -3 этажа на отметке -11,400
М 1 : 200

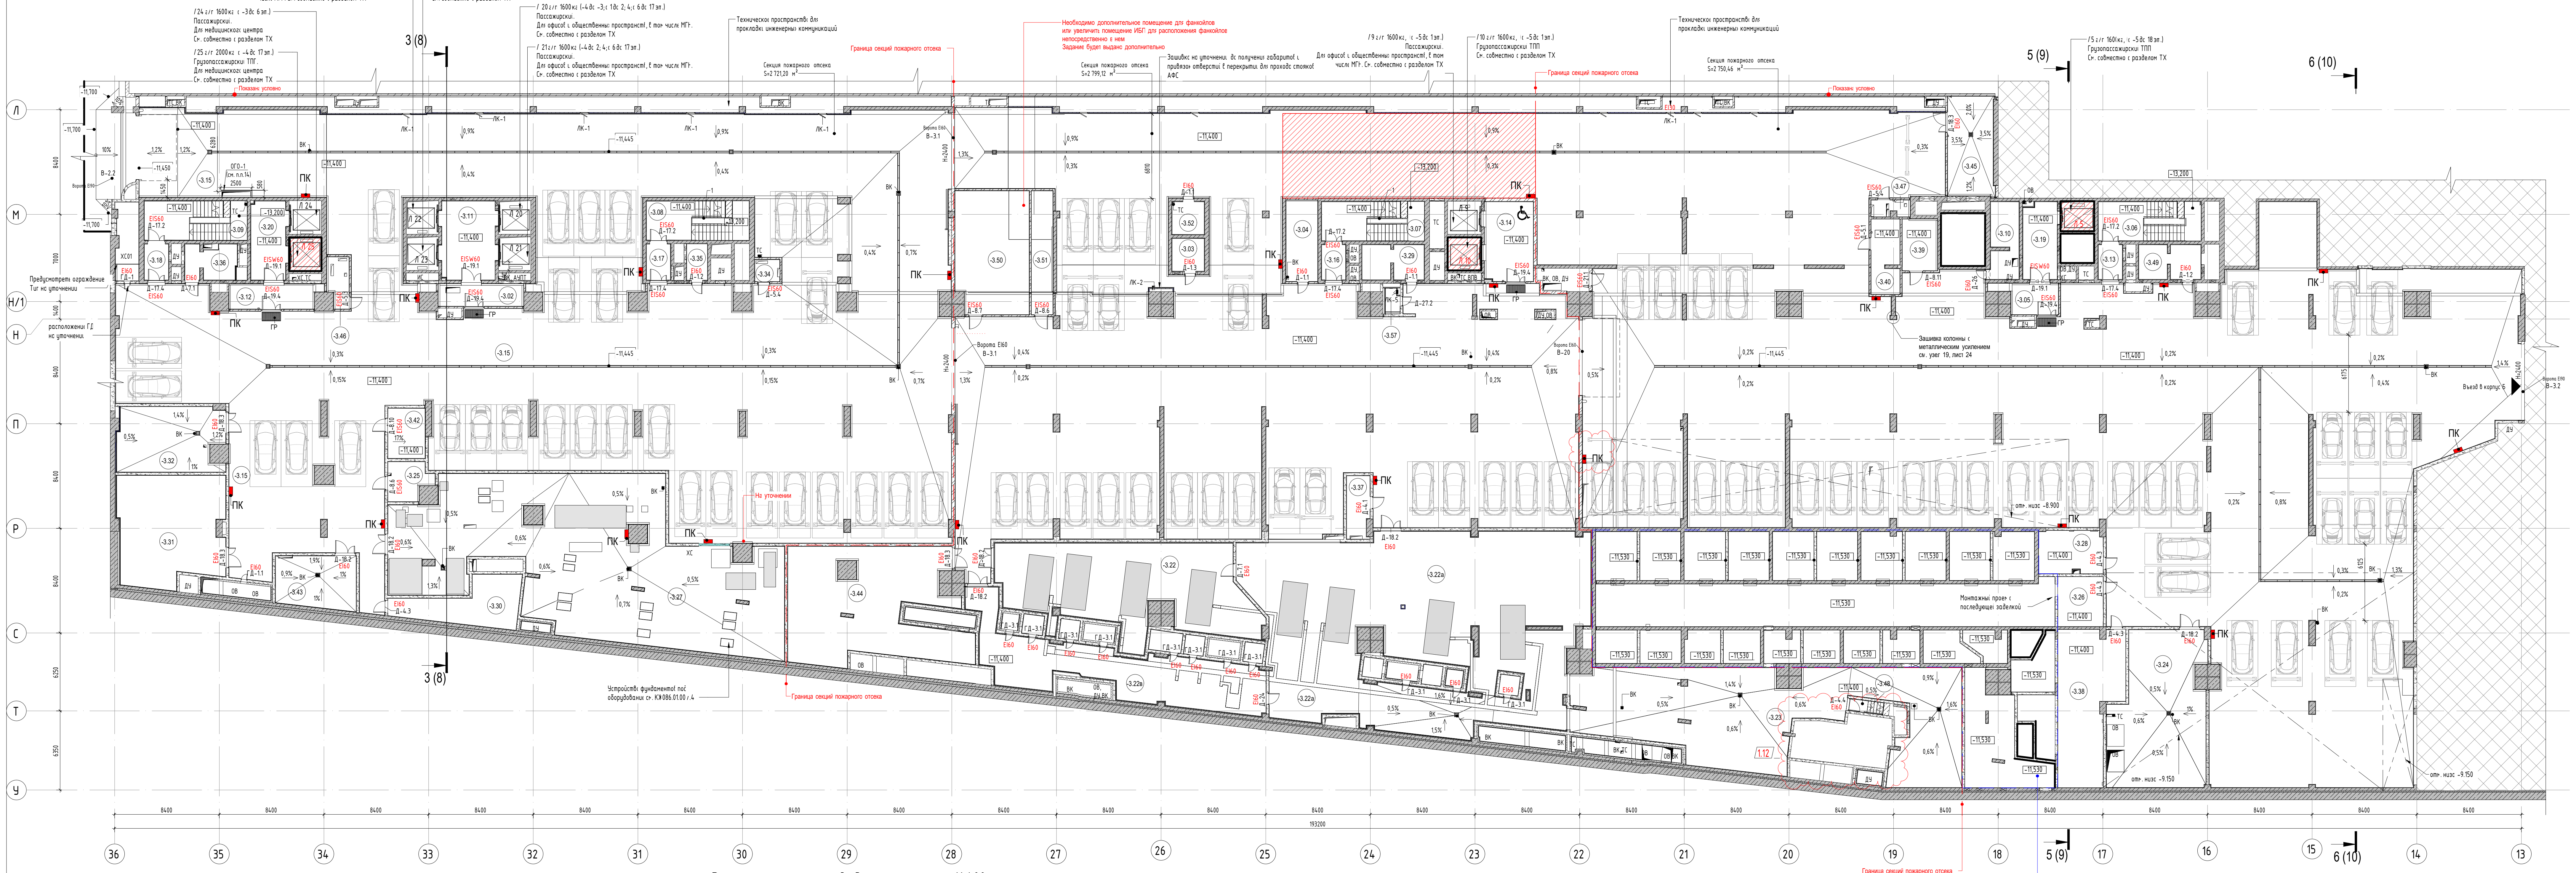
Л
М
Н/1
Н
П
Р
С
Т
У
36
35
34
33
32
31
30
29
28
27
26
25
24
23
22
21
20
19
18
17
16
15
14
13
3 (8)
5 (9)
6 (10)
8400
193200
Граница секций пожарного отсека
Необходимо дополнительное помещение для фанкойлов или увеличить помещение ИБП для расположения фанкойлов непосредственно в нем
Задание будет выдано дополнительно
Секция пожарного отсека S=2 799,12 м²
Граница секций пожарного отсека
Площадь пожарной секции входит в состав отсека на -2 этаже
ПК
Гр
1.11
1.12

Экспликация помещений -3 этажа на отм. -11,400

Номер помещения	Наименование	Площадь, м²	Кат. пом.
01.Автостоянка			
-3.01	Помещение хранения автомобилей на 107 м/м	3587,71	В2
-3.15	Помещение хранения автомобилей на 44 м/м	1743,90	В2
		5331,60	
14.Вспомогательные помещения			
-3.04	Помещение хранения пожарного инвентаря	16,77	В4
-3.10	Помещение хранения пожарного инвентаря	12,84	В4
-3.38	Склад оборудования	56,03	В2
-3.52	Помещение хранения пожарного инвентаря	6,91	В4
		92,55	
15.1Санузлы			
-3.57	Санузел	2,04	-
		2,04	
15.Места общего пользования			
-3.02	Тамбур-шлюз	11,76	-
-3.05	Тамбур-шлюз	10,98	-
-3.06	Лестничная клетка 2	25,98	-
-3.07	Лестничная клетка 3	25,97	-
-3.08	Лестничная клетка 4	25,97	-
-3.09	Лестничная клетка 5	25,95	-
-3.11	Лифтовый холл	27,76	-
-3.12	Тамбур-шлюз	14,53	-
-3.13	Тамбур-шлюз	5,54	-

1.11

Экспликация помещений -3 этажа на отм. -11,400

Номер помещения	Наименование	Площадь, м²	Кат. пом.
-3.14	Лифтовый холл/зона безопасности	25,71	-
-3.16	Тамбур-шлюз	5,66	-
-3.17	Тамбур-шлюз	5,76	-
-3.18	Тамбур-шлюз	5,70	-
-3.19	Лифтовый холл	16,60	-
-3.20	Лифтовый холл	17,20	-
		251,05	
16.Инженерные помещения			
-3.03	Помещение уборочной техники	6,94	В4
-3.22	Дизель-генераторная	126,86	В1
-3.22а	Дизель-генераторная	360,59	В1
-3.22в	Помещение хранения резервного запаса диз.топлива	88,09	В1
-3.23	Венткамера	194,41	Д
-3.24	Венткамера	86,50	Д
-3.25	Помещение для размещения оборудования кондиционирования и АУГПТ	9,80	В4
-3.26	Помещение хранения пожарного инвентаря	14,56	В3
-3.27	Холодильный центр	300,05	В3
-3.28	Электрощитовая подземной автостоянки	17,51	В3
-3.29	Электрощитовая	13,89	В3
-3.30	Электрощитовая подземной автостоянки	28,55	В3
-3.31	Венткамера	72,31	В3

Экспликация помещений -3 этажа на отм. -11,400

Номер помещения	Наименование	Площадь, м²	Кат. пом.
-3.32	Венткамера	43,42	Д
-3.34	Помещение вертикальных коммуникаций ИТ и СС	3,64	В4
-3.35	Электрощитовая	4,83	В4
-3.36	Электрощитовая	11,15	В3
-3.37	Электрощитовая подземной автостоянки	9,20	В4
-3.39	КУ АСО	11,86	В3
-3.40	Помещение для размещения оборудования кондиционирования и АУГПТ	13,82	В3
-3.42	КУ АСО	12,19	В3
-3.43	Венткамера	27,06	Д
-3.44	Венткамера	113,00	В1
-3.45	Помещение КНС	29,72	Д
-3.46	Помещение вертикальных коммуникаций ИТ и СС	6,85	В4
-3.47	Помещение вертикальных коммуникаций ИТ и СС	4,05	В4
-3.48	Лестничная клетка 10	5,74	-
-3.49	Электрощитовая	13,65	В3
-3.50	Помещение ИБП	52,74	В3
-3.51	Помещение для оборудования кондиционирования и АУГПТ	17,44	В3
		1700,43	
Итого		7377,67	

Ведомость машиномест -3 этаж

Наименование	Кол-во, шт.
Машино-место 5300х2500мм. Средний класс	74
Машино-место 5300х2500мм. Малый класс	15
	89

Условные обозначения:

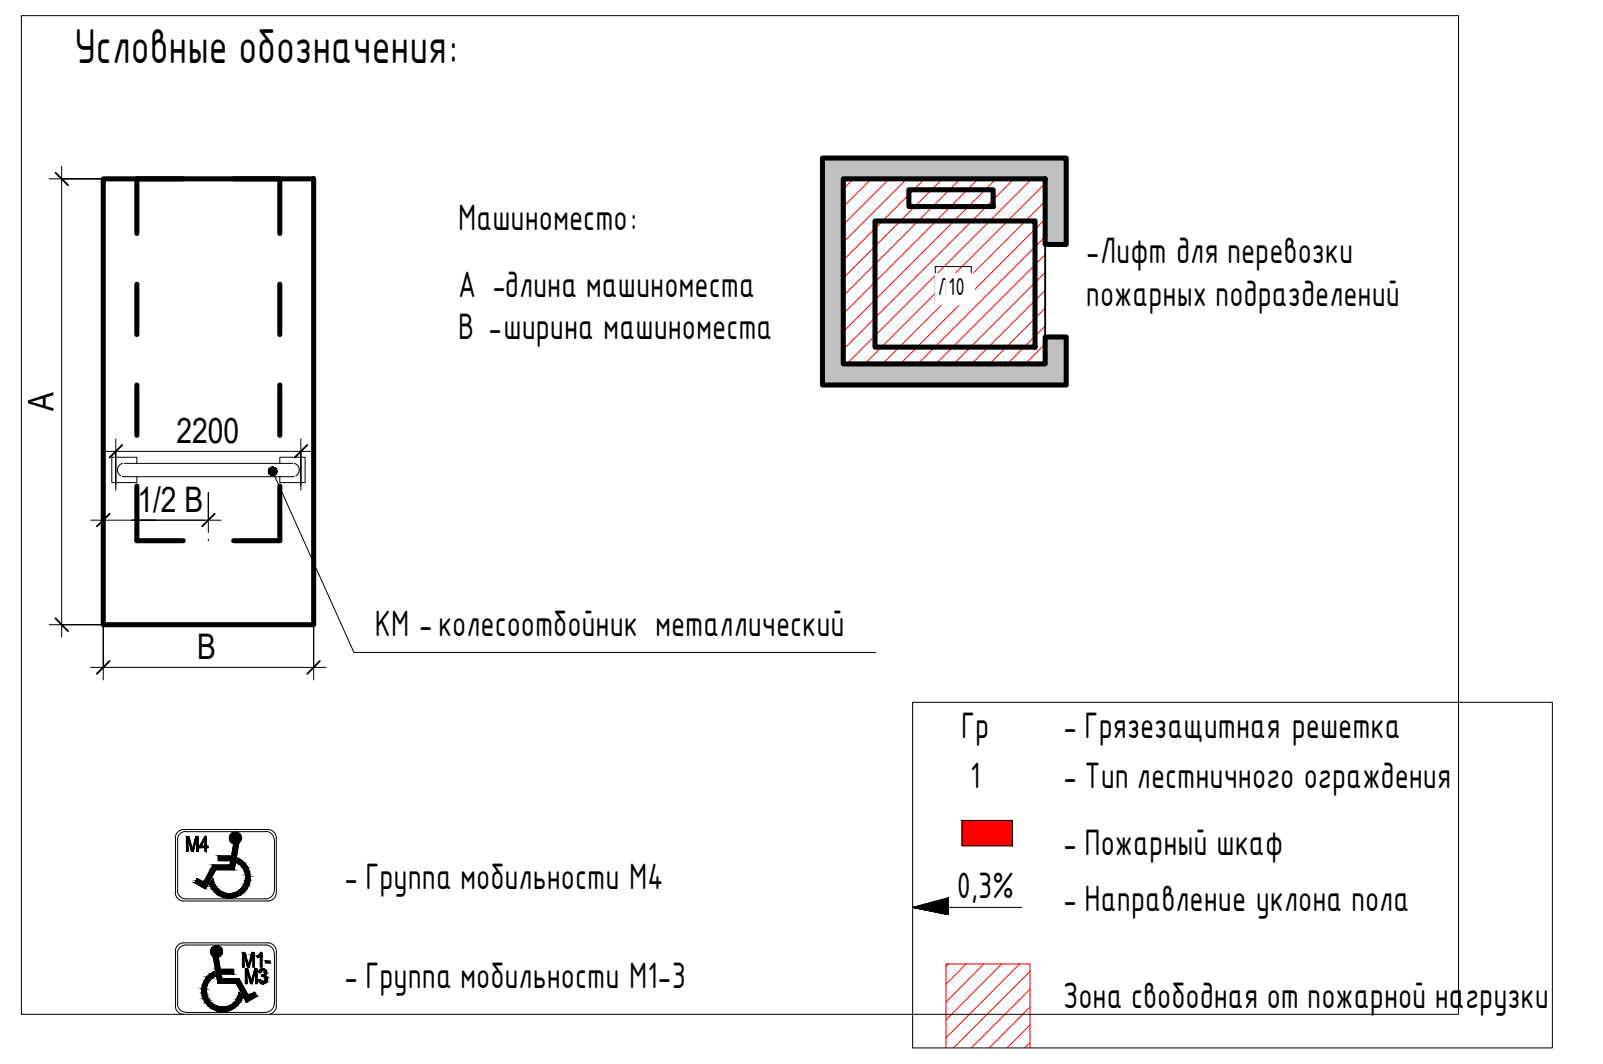

Машиноместо:

A -длина машиноместа
B -ширина машиноместа

-Лифт для перевозки пожарных подразделений

КМ - колесоотбойник металлический

- Группа мобильности М4
- Группа мобильности М1-3

Гр	- Грязезащитная решетка
1	- Тип лестничного ограждения
🟥	- Пожарный шкаф
0,3%	- Направление уклона пола
▨	Зона свободная от пожарной нагрузки

Схема блокировки корпусов

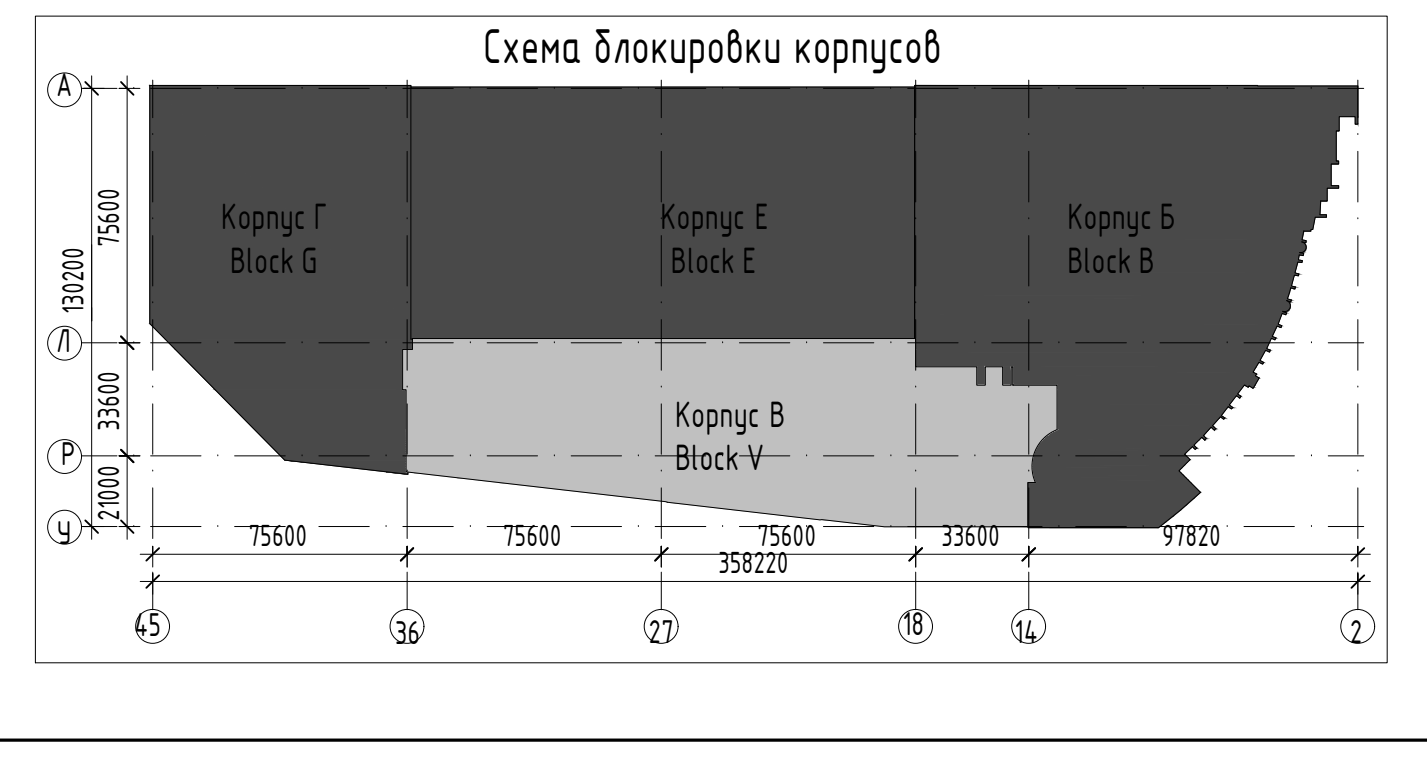

1. Лист смотреть совместно с л. 7-11.
2. Схемы дверных блоков и спецификацию элементов заполнения проемов смотреть на л. 12.
3. Ведомость отделки помещений смотреть на л. 37.
4. План полов смотреть на л. 26, 26.1, 26.2, 26.3, 26.4. Экспликация полов дана на л. 27.
5. Стояки и воздуховоды зашить по месту. Расход материала смотри спецификацию расхода материалов на л. 24 настоящего альбома.
6. Против ревизий на стояках канализации в коробах зашивки предусмотреть по месту установку нажимных люков под плитку размером 300х400h на высоте 800 мм от чистого пола в помещениях с отделкой стен плиткой; декоративных нажимных люков в помещениях со стенами под покраску.
7. Коммуникации, зашитые ГКЛ и кирпичной кладкой, оборудовать лючками с нажимным механизмом, согласно пункта 6. Замком оборудовать двери для входа в ниши коммуникаций.
8. Направляющие ЗД-1 смотри раздел: Строительное задание Корпус В от "Гарантэнерго" Шифр: 5КС-АТК-СЗ.
9. Ведомость окраски стен помещний автостоянки см. л. 37.
10. Выполнить затирку цементно-песчаным раствором до достижения ровной гладкой поверхности, как по горизонтали, так и по вертикали с последующим нанесением одного слоя шпатлевки.
11. Расстановку машиномест их привязки, узел устройства колесоотбойников и их точное размещение см. СБД-КУТ03-КМП-2-25-Р-100-ТХ.01.00. Технологические решения. Подземная автостоянка.
12. Корректировка данного листа выполнена на основании исходных данных раздела АР. СБД-1276-ПК-КУТ03-0000-АР01.00, выполненной компанией ТПО "Прайд".
13. Маркировка и грузоподъемность лифтов указаны на основании Приложения №5 "Схема вертикального транспорта Корпуса В" к официальному письму от ООО "СБД" от 06.02.2024 № КУТ06-06_392 "О направлении требований к корректировке РД по -1, -2, -3, -4, -5 эт."
14. Ограждение "ОГО-1" выполнить согласно указаным размерам 2500х580 (h=1000мм) и согласно документации "СЭ 18245-05.26- ПП". Смотреть совместно с листом 18 данного комплекта.

С выпуском данного листа аннулировать лист №3 Прайдекс Констракшн шифр PR-200.СБВ.АР01.00 (изм.3. 12.23).

0,000 = 147,500

КУТ03-Р-ПИР-2-26-100 - АР01.01.00

Реконструкция делового комплекса в составе корп. «А», «Б», «В», «Г», «Е» с единой стилобатной (подземной) частью и устройством надземной объединительной аркады по адресу: пересечение Кутузовского проспекта и улицы Кульнева, район Дорогомилово, Западный административный округ города Москвы

Изм.	Кол уч.	Лист	№ док.	Подпись	Дата
Разработал		Рыбальченко			24.03.26
Проверил		Бугакова			24.03.26
ГАП		Пичурова			24.03.26
ГИП		Хорлуков			24.03.26
Н.контроль		Пичурова			24.03.26

Архитектурные решения. Подземная автостоянка (Стилобат)

Стадия	Лист	Листов
Р	4	

План -3 этажа на отметке -11,400

MARKS ENGINEERING

Формат А2х3

Согласовано

Взам. инв. №

Подп. и дата

Инв. № подл.