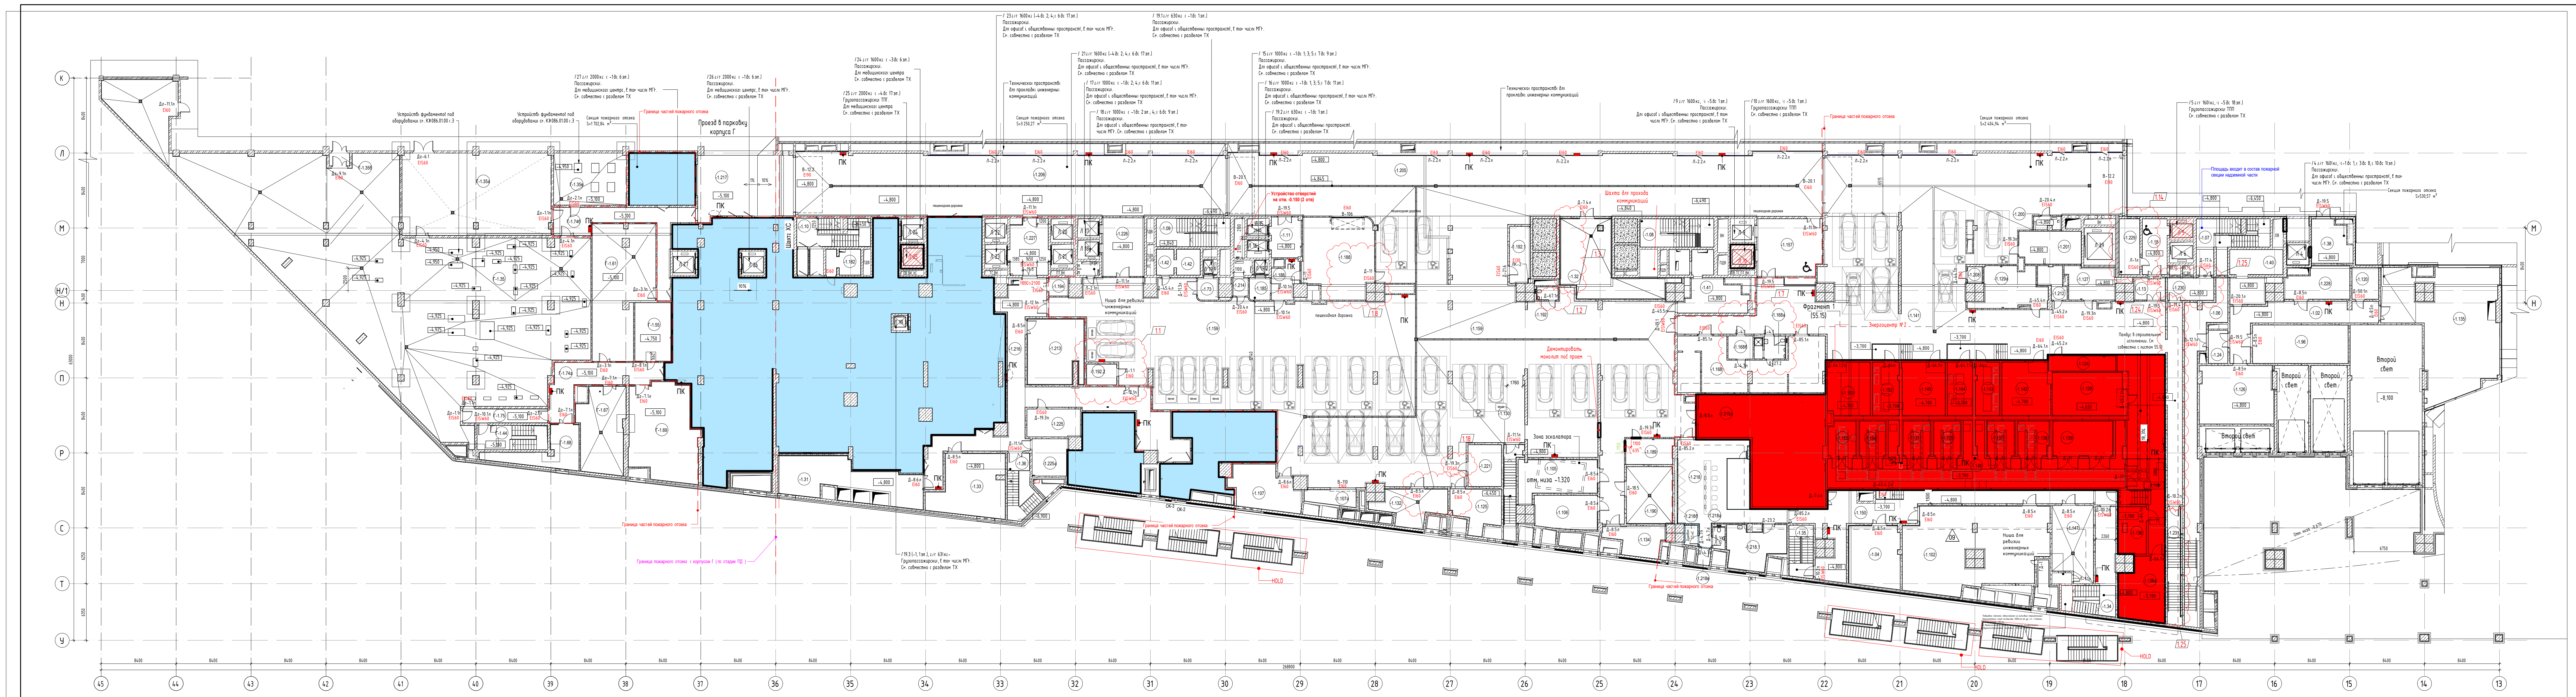

Экспликация помещений_Корпус В - 1 этажа

Номер помещения	Наименование	Площадь, м²	Кат. пом.
01.Автостоянка			
-1.141	Автостоянка	821,41	В2
-1.159	Автостоянка	1242,78	В2
-1.205	Помещение проезда в автостоянку	460,28	В2
-1.206	Помещение проезда в автостоянку	329,84	В2
-1.217	Помещение проезда в автостоянку Корпуса Г	58,56	В2
		2912,87	
02.Банк ВСП Массовый сегмент			
-1.185	Лифтовый холл	5,76	-
-1.186	Тамбур-шлюз	11,52	-
-1.188	Инкасация	68,03	-
		85,32	
14.Вспомогательные помещения			
-1.134	Раздевалка	18,62	-
-1.190	Помещение охраны	32,97	-
-1.192.1	Пост охраны	14,58	
-1.192.2	Помещение уборочной техники	7,89	В4
		74,06	
15.1Санузлы			
-1.192	Санузел	3,47	-
		3,47	
15.Места общего пользования			
-1.02	Коридор	47,74	-
-1.06	Лестничная клетка 11	71,53	-

1.11

1.11

Экспликация помещений_Корпус В - 1 этажа

Номер помещения	Наименование	Площадь, м²	Кат. пом.
-1.07	Лестничная клетка 2	21,71	-
-1.08	Лестничная клетка 3	26,04	-
-1.09	Лестничная клетка 4	26,04	-
-1.10	Лестничная клетка 5	25,19	-
-1.11	Лифтовый холл/ тамбур-шлюз	15,23	-
-1.13	Тамбур-шлюз	9,00	-
-1.18	Лифтовый холл/зона безопасности	17,27	-
-1.24	Тамбур-шлюз	8,11	-
-1.34	Лестничная клетка 6	38,92	-
-1.35	Лестничная клетка 7	15,68	-
-1.36	Лестничная клетка 8	21,49	-
-1.38	Лифтовый холл/ тамбур-шлюз	19,79	-
-1.73	Лифтовый холл/тамбур-шлюз	5,81	-
-1.130	Лестничная клетка 9	15,43	-
-1.150	Коридор	91,78	-
-1.157	Лифтовый холл/тамбур-шлюз/зона безопасности	45,29	-
-1.216	Коридор	132,71	-
-1.226	Лифтовый холл/ тамбур-шлюз	30,86	-
-1.227	Лифтовый холл/тамбур-шлюз	25,78	-
-1.230	Тамбур-шлюз	13,10	-

Экспликация помещений_Корпус В - 1 этажа

Номер помещения	Наименование	Площадь, м²	Кат. пом.
-1.231	Лестничная клетка 12	18,96	
		743,48	
16.Инженерные помещения			
-1.04	Венткамера	38,88	Д
-1.31	Венткамера	57,63	В3
-1.32	Венткамера	63,24	В3
-1.33	Венткамера	51,18	В3
-1.40	Электрощитовая ППУ	30,37	В3
-1.41	Электрощитовая ППУ	37,43	В3
-1.42	Электрощитовая офисов	13,52	В3
-1.96	Помещение для жироуловителей	46,63	В3
-1.102	Венткамера	137,26	В2
-1.105	Венткамера	35,14	В3
-1.106	Венткамера	26,33	В3
-1.107	Венткамера	33,95	В3
-1.107а	Венткамера	9,54	В3
-1.120	Техпомещение вакуумного мусороудаления	10,66	В3
-1.124	Помещение для фанкойлов и Газ.балона	12,78	В3
-1.125	Венткамера	22,76	В2
-1.126	Венткамера	53,75	В3
-1.127	АО АиСС	21,15	В3

Экспликация помещений_Корпус В - 1 этажа

Номер помещения	Наименование	Площадь, м²	Кат. пом.
-1.129	Электрощитовая	39,79	В3
-1.129а	Электрощитовая	31,56	В3
-1.131	Трансформаторная камера	13,22	В3
-1.132	Венткамера	25,99	В2
-1.133	Трансформаторная камера	12,90	В4
-1.135	Венткамера	138,33	В2
-1.136	Электрощитовая	16,81	В3
-1.136а	Электрощитовая	37,14	В3
-1.137	Трансформаторная камера	13,10	В4
-1.138	Трансформаторная камера	14,83	В4
-1.139	2ИБП ЭЦ2	28,11	В3
-1.142	ГРЩ-20В	31,77	В3
-1.143	ТП20, РУ-20 кВ	16,56	В3
-1.144	ТП19, РУ-20 кВ	17,13	В3
-1.145	ГРЩ-19В	28,78	В3
-1.147	Венткамера	36,84	В3
-1.148	Коридор	130,10	-
-1.152	ТП18, РУ-20 кВ	18,23	В3
-1.153	ГРЩ-18В	28,36	В3
-1.154	Трансформаторная камера	12,59	В4

1.11

1.11

1.11

Экспликация помещений_Корпус В - 1 этажа

Номер помещения	Наименование	Площадь, м²	Кат. пом.
-1.155	Трансформаторная камера	13,16	В4
-1.182	Электрощитовая	10,68	В3
-1.189	Кроссовая при ЦПБ	15,45	В3
-1.194	Помещение коммуникаций СС (слаботочных систем) - ППС	4,45	В4
-1.200	Помещение вертикальных коммуникаций ИТ и СС	4,52	В4
-1.201	КУ АСО	25,19	В3
-1.208	Тех. помещение для кондиционеров	3,01	В4
-1.212	Помещение для фанкойлов и газ. балона	8,98	В4
-1.213	Венткамера	44,63	В3
-1.214	Помещение вертикальных коммуникаций ИТ и СС	7,24	В4
-1.215а	1 ИБП ЭЦ 2	131,02	В3
-1.221	КУ АСО	17,60	В3
-1.225	Кроссовая КУ АСО	18,39	В3
-1.225а	Помещение для размещения оборудования кондиционирования и АУГПТ	16,16	В3
-1.228	Венткамера	24,53	В3
-1.229	Помещение для прокладки инженерных коммуникаций	14,38	
		1753,69	
20. Зона ЦПБ			
-1.218	ЦПБ	83,89	В3
-1.218.1	Комната отдыха ЦПБ	37,98	В3

Экспликация помещений_Корпус В - 1 этажа

Номер помещения	Наименование	Площадь, м²	Кат. пом.
-1.218а	Санузел	3,25	-
-1.218б	Душевая	3,31	-
-1.218в	Гардероб	2,54	-
		130,97	
21. Помещения для отдыха водителей			
-1.168	Помещение для отдыха водителей	83,12	-
-1.168а	Санузел с душевой	8,03	-
-1.168б	Комната для сна водителей	7,07	-
		98,21	
Итого		5802,08	

Экспликация помещений_Корпус Г - 1 этажа

Номер помещения	Наименование	Площадь, м²	Кат. пом.
15.Места общего пользования			
Г-1.35б	Тамбур	3,16	-
Г-1.44	Лестничная клетка 6	21,39	
Г-1.74а	Коридор	39,73	
Г-1.74б	Коридор	45,61	
Г-1.74в	Коридор	44,88	
Г-1.75	Тамбур-шлюз	15,04	
		169,81	
16.Инженерные помещения			
Г-1.35	ИТП	812,33	
Г-1.35а	Помещение баков ГВС	152,70	
Г-1.35в	Насосная пожаротушения	47,20	Д
Г-1.61	Помещение водоподготовки	90,10	
		1102,33	
Технические помещения			
Г-1.55	Электрощитовая ВРУ/ППУ	26,97	В3
Г-1.67	Венткамера	47,39	В2
Г-1.68	Венткамера	25,78	В3
Г-1.69	Венткамера	76,40	В3
		176,54	
Итого		1448,69	

1.11

1.11

Ведомость машиномест -1 этаж

Наименование	Кол-во, шт.
Машино-место 6000x3750мм. Большой класс	1
Машино-место 6000x3600мм (МГН группы М4)	17
Машино-место зависимое 6000x3750мм. Большой класс	4
Машино-место зависимое 5300x2500мм. Малый класс	2
Машино-место 5300x2500мм (МГН группы М1-М3)	6
	30

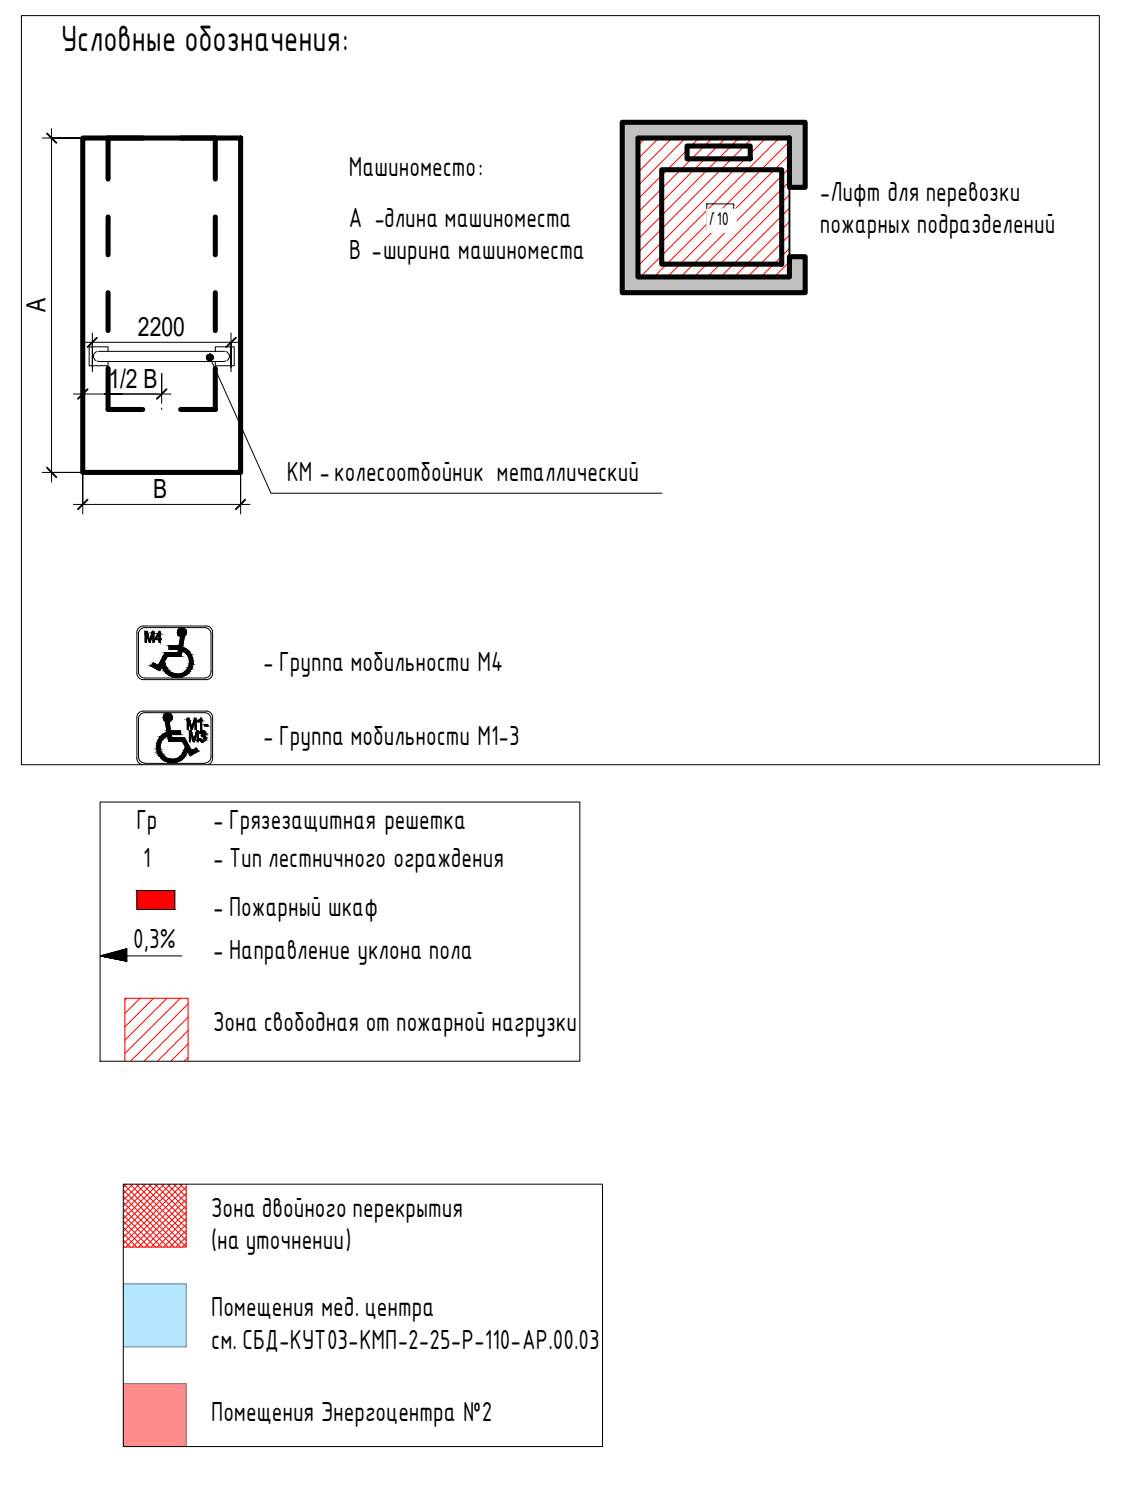

Условные обозначения:

Машиноместо:
A -длина машиноместа
B -ширина машиноместа

КМ - колесоотбойник металлический

-Лифт для перевозки пожарных подразделений

- Группа мобильности М4
- Группа мобильности М1-3

Гр	- Грязезащитная решетка
1	- Тип лестничного ограждения
🟥	- Пожарный шкаф
0,3%	- Направление уклона пола
▨	Зона свободная от пожарной нагрузки

▨	Зона двойного перекрытия (на уточнении)
🟦	Помещения мед. центра см. СБД-КУТ03-КМП-2-25-Р-110-АР.00.03
🟥	Помещения Энергоцентра №2

1. Лист смотреть совместно с л. 7-11.
2. Схемы дверных блоков и спецификацию элементов заполнения проемов смотреть на л. 12.
3. Ведомость отделки помещений смотреть на л. 37.
4. План полов смотреть на л. 26, 26.1, 26.2, 26.3, 26.4. Экспликация полов дана на л. 27.
5. Стояки и воздуховоды зашить по месту. Расход материала смотри спецификацию расхода материалов на л. 24 настоящего альбома.
6. Против ревизий на стояках канализации в коробах зашивки предусмотреть по месту установку нажимных люков под плитку размером 300х400h на высоте 800 мм от чистого пола в помещениях с отделкой стен плиткой; декоративных нажимных люков в помещениях со стенами под покраску.
7. Коммуникации, зашитые ГКЛ и кирпичной кладкой, оборудовать лючками с нажимным механизмом, согласно пункта 6. Замком оборудовать двери для входа в ниши коммуникаций.
8. Направляющие ЗД-1 смотри раздел: Строительное задание Корпус В от "Гарантэнерго" Шифр: 5КС-АТК-СЗ.
9. Ведомость окраски стен помещний автостоянки см. л. 37.
10. Выполнить затирку цементно-песчаным раствором до достижения ровной гладкой поверхности, как по горизонтали, так и по вертикали с последующим нанесением одного слоя шпатлевки.
11. Расстановку машиномест их привязки, узел устройства колесоотбойников и их точное размещение см. СБД-КУТ03-КМП-2-25-Р-100-ТХ.01.00. Технологические решения. Подземная автостоянка.
12. Корректировка данного листа выполнена на основании исходных данных раздела АР. СБД-1276-ПК-КУТ03-0000-АР01.00, выполненной компанией ТПО "Прайд".
13. Маркировка и грузоподъемность лифтов указаны на основании Приложения №5 "Схема вертикального транспорта Корпуса В" к официальному письму от ООО "СБД" от 06.02.2024 № КУТ06-06_392 "О направлении требований к корректировке РД по -1, -2, -3, -4, -5 эт."
14. Ограждение "ОГО-1" выполнить согласно указаным размерам 2500х580 (h=1000мм) и согласно документации "СЭ 18245-05.26- ПП". Смотреть совместно с листом 18 данного комплекта.

С выпуском данного листа аннулировать лист №3 Прайдекс Констракшн шифр PR-200.СБВ.АР01.00 (изм.3. 12.23).

Схема блокировки корпусов

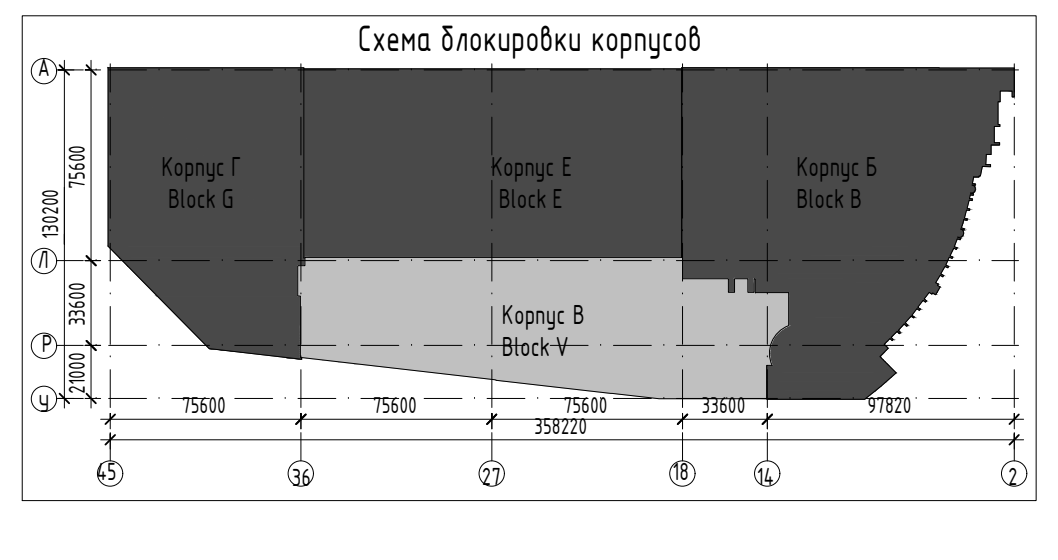

0,000 = 147,500

1		Изм.	3932/26		06.26	КУТ03-Р-ПИР-2-26-100 - АР01.01.00
Изм.	Кол уч.	Лист	№ док.	Подпись	Дата	Реконструкция делового комплекса в составе корп. «А», «Б», «В», «Г», «Е» с единой стилобатной подземной частью и устройством надземной объединительной аркады по адресу: пересечение Кутузовского проспекта и улицы Кульнева, район Дорогомилово, Западный административный округ города Москвы
Разработал	Бугакова				24.03.26	Архитектурные решения. Подземная автостоянка (Стилобат)
Проверил	Бугакова				24.03.26	
ГАП	Пичурова				24.03.26	План -1 этажа на отметке -4,800
ГИП	Хорлуков				24.03.26	
Н.контроль	Пичурова				24.03.26	

Стадия	Лист	Листов
Р	6	

MARKS ENGINEERING

Формат А2х4