План -3 этажа
М 1:200

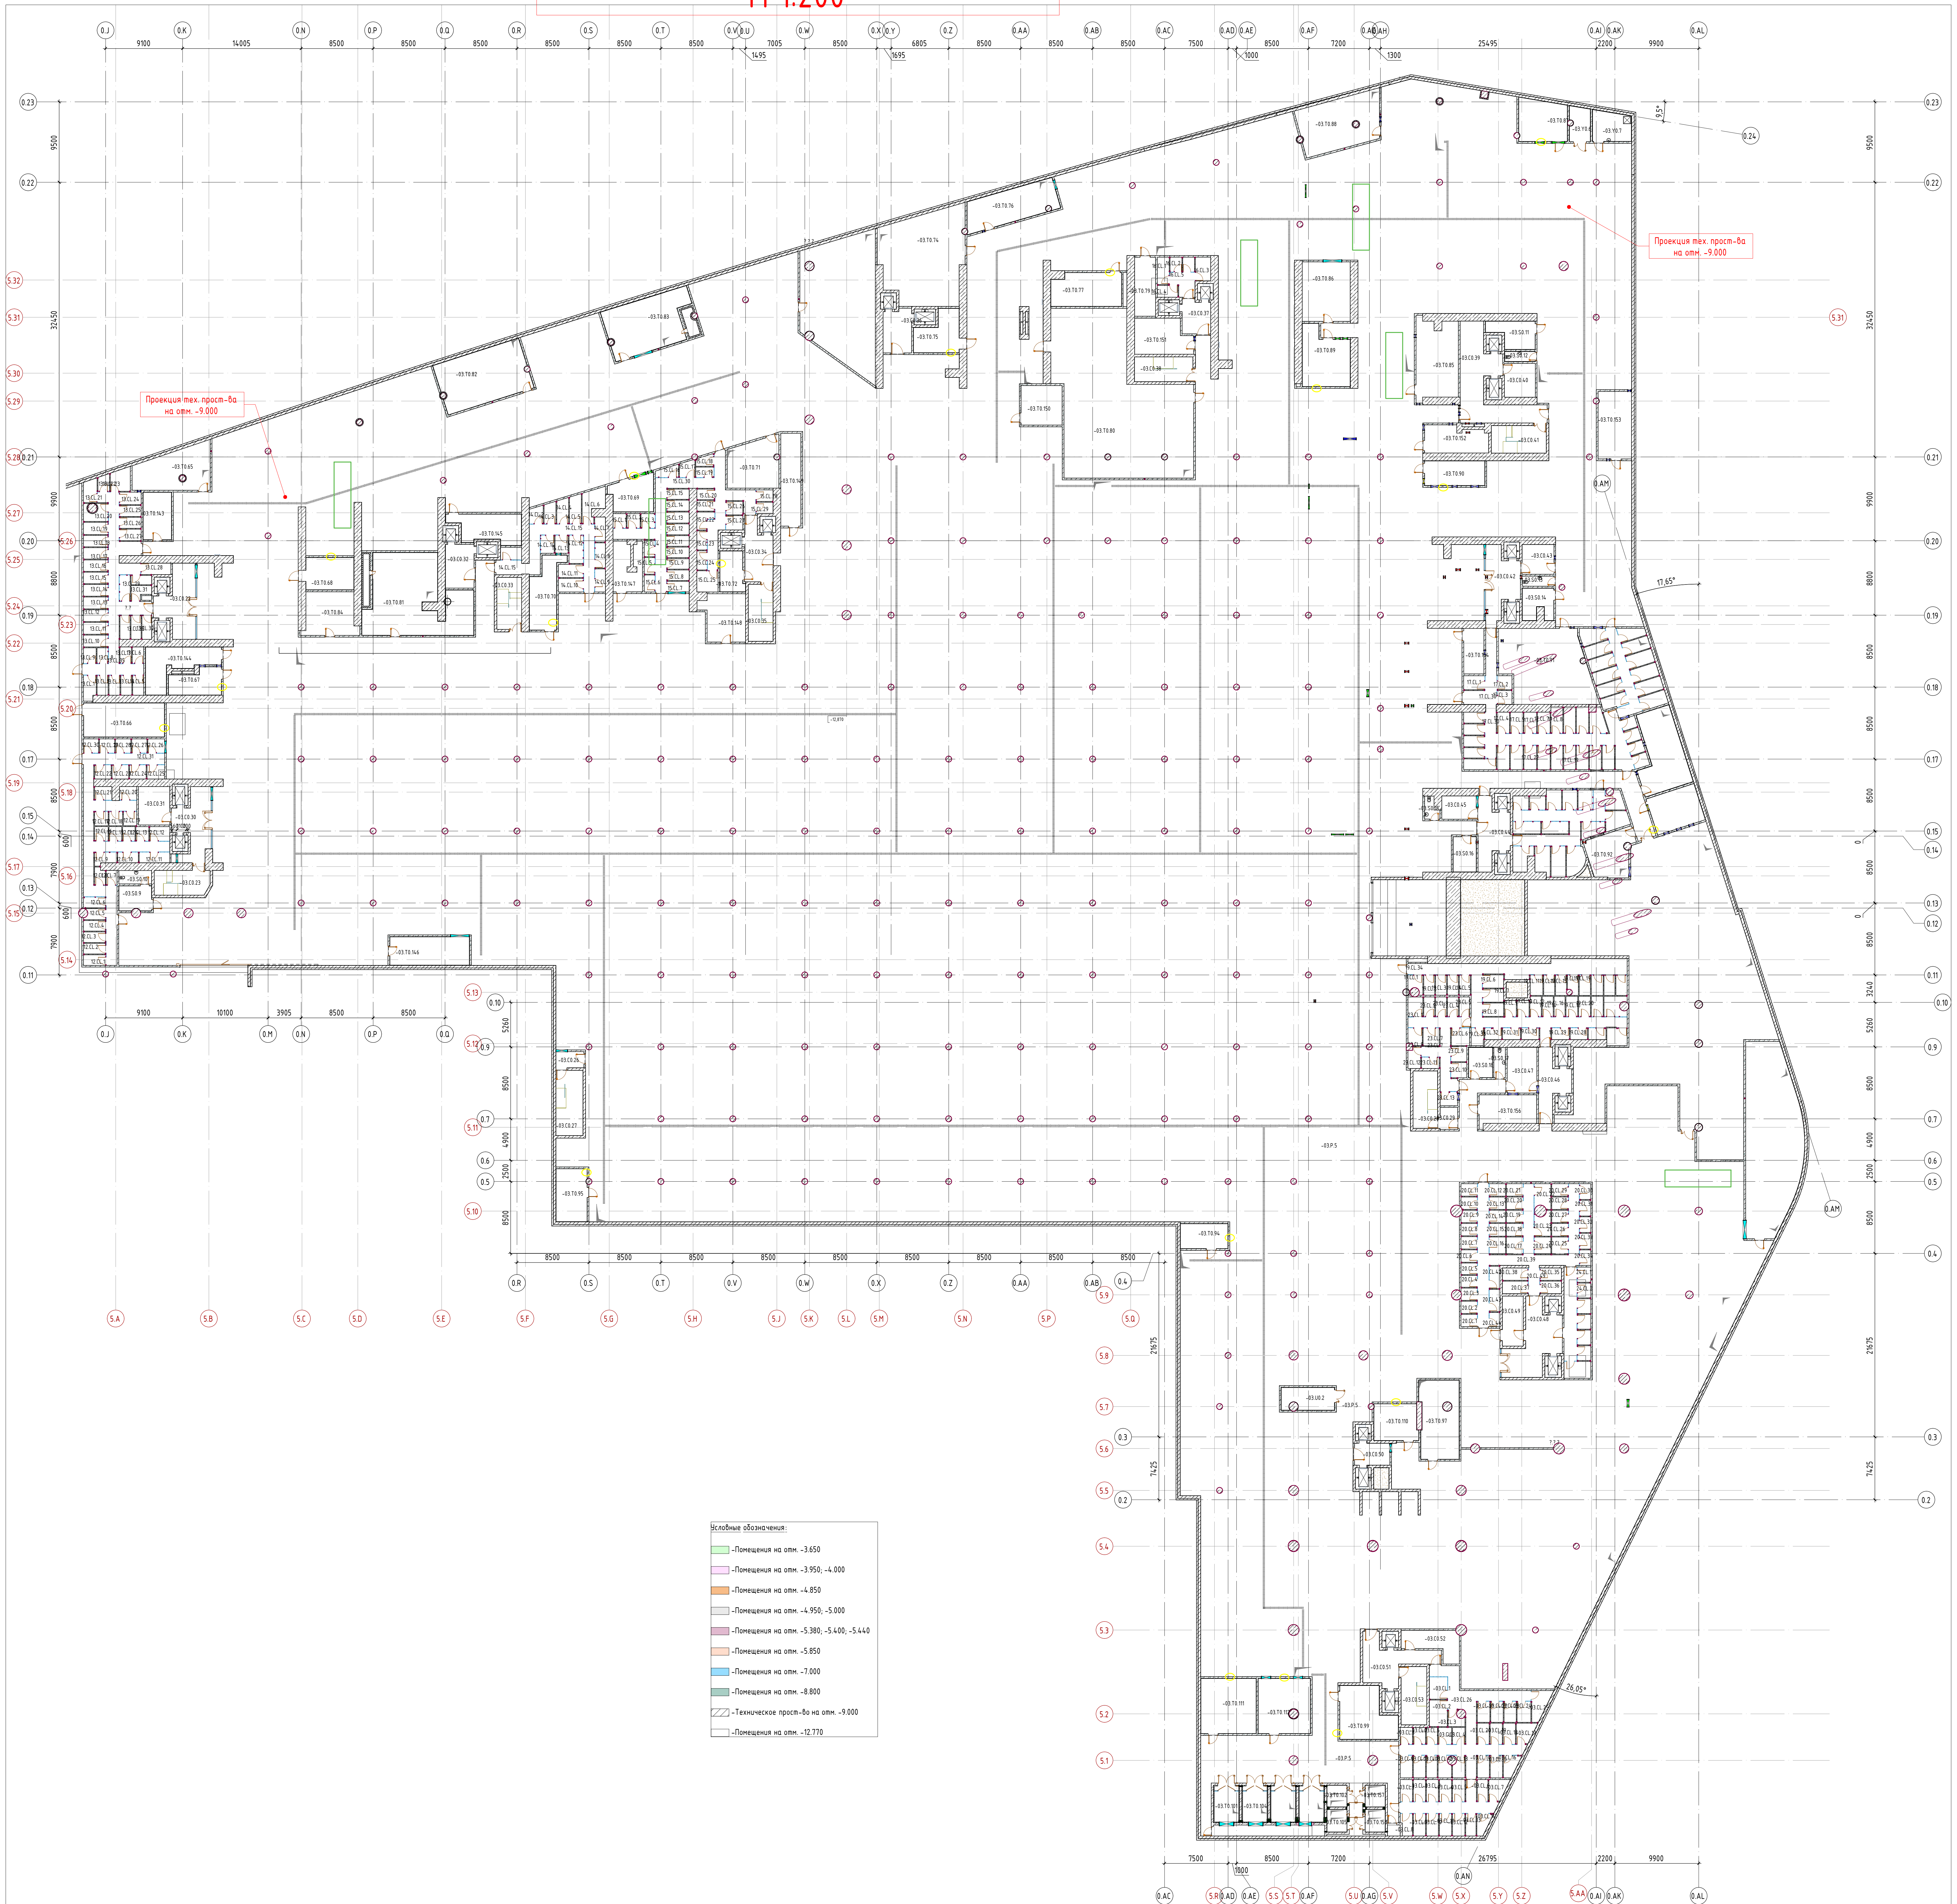
Проекция тех. прост-ва на отм. -9.000
Проекция тех. прост-ва на отм. -9.000

Условные обозначения:

- 🟩 -Помещения на отм. -3.650
- 🟪 -Помещения на отм. -3.950; -4.000
- 🟧 -Помещения на отм. -4.850
- ⬜ -Помещения на отм. -4.950; -5.000
- 🟪 -Помещения на отм. -5.380; -5.400; -5.440
- 🟧 -Помещения на отм. -5.850
- 🟦 -Помещения на отм. -7.000
- 🟩 -Помещения на отм. -8.800
- ▨ -Техническое прост-во на отм. -9.000
- ☐ -Помещения на отм. -12.770

Экспликация помещений -3 этажа

№ пом.	Наименование	Площадь, м²	Кат. пом.
Блок кладовых -03.CL.12			
12.CL.1	Кладовая	3,30	В2
12.CL.2	Кладовая	3,30	В2
12.CL.3	Кладовая	3,30	В2
12.CL.4	Кладовая	3,30	В2
12.CL.5	Кладовая	3,10	В2
12.CL.6	Кладовая	3,50	В2
12.CL.7	Кладовая	2,30	В2
12.CL.8	Кладовая	2,50	В2
12.CL.9	Кладовая	3,60	В2
12.CL.10	Кладовая	3,10	В2
12.CL.11	Кладовая	4,60	В2
12.CL.12	Кладовая	4,10	В2
12.CL.13	Кладовая	2,60	В2
12.CL.14	Кладовая	2,50	В2
12.CL.15	Кладовая	2,60	В2
12.CL.16	Кладовая	2,80	В2
12.CL.17	Кладовая	2,80	В2
12.CL.18	Кладовая	2,80	В2
12.CL.19	Кладовая	2,70	В2
12.CL.20	Кладовая	3,30	В2
12.CL.21	Кладовая	3,30	В2
12.CL.22	Кладовая	3,30	В2
12.CL.23	Кладовая	3,30	В2
12.CL.24	Кладовая	3,30	В2
12.CL.25	Кладовая	3,50	В2
12.CL.26	Кладовая	3,40	В2
12.CL.27	Кладовая	3,10	В2
12.CL.28	Кладовая	3,10	В2
12.CL.29	Кладовая	3,10	В2
12.CL.30	Кладовая	3,00	В2
12.CL.31	Проход	64,00	В2
		158,50	
Блок кладовых под аренду -03.CL.13			
13.CL.1	Кладовая под аренду	4,40	В2
13.CL.2	Кладовая под аренду	3,10	В2
13.CL.3	Кладовая под аренду	3,10	В2
13.CL.4	Кладовая под аренду	3,10	В2
13.CL.5	Кладовая под аренду	3,10	В2
13.CL.6	Кладовая под аренду	2,70	В2
13.CL.7	Кладовая под аренду	2,70	В2
13.CL.8	Кладовая под аренду	2,50	В2
13.CL.9	Кладовая под аренду	2,80	В2
13.CL.10	Кладовая под аренду	4,10	В2
13.CL.11	Кладовая под аренду	4,10	В2
13.CL.12	Кладовая под аренду	4,10	В2
13.CL.13	Кладовая под аренду	4,10	В2
13.CL.14	Кладовая под аренду	4,10	В2
13.CL.15	Кладовая под аренду	4,00	В2
13.CL.16	Кладовая под аренду	4,00	В2
13.CL.17	Кладовая под аренду	4,00	В2
13.CL.18	Кладовая под аренду	4,00	В2
13.CL.19	Кладовая под аренду	4,30	В2
13.CL.20	Кладовая под аренду	5,00	В2
13.CL.21	Кладовая под аренду	4,30	В2
13.CL.22	Кладовая под аренду	2,60	В2
13.CL.23	Кладовая под аренду	6,10	В2
13.CL.24	Кладовая под аренду	3,90	В2
13.CL.25	Кладовая под аренду	3,40	В2
13.CL.26	Кладовая под аренду	3,40	В2
13.CL.27	Кладовая под аренду	3,50	В2
13.CL.28	Кладовая под аренду	4,80	В2
13.CL.29	Кладовая под аренду	2,80	В2
13.CL.30	Кладовая под аренду	4,10	В2
13.CL.31	Кладовая под аренду	3,50	В2
13.CL.32	Кладовая под аренду	3,30	В2
13.CL.33	Кладовая под аренду	3,50	В2
13.CL.34	Кладовая под аренду	3,50	В2
13.CL.35	Проход	50,80	В2
		176,80	
Блок кладовых -03.CL.14			
14.CL.1	Кладовая	3,80	В2
14.CL.2	Кладовая	3,30	В2
14.CL.3	Кладовая	3,50	В2
14.CL.4	Кладовая	4,10	В2
14.CL.5	Кладовая	4,80	В2
14.CL.6	Кладовая	8,30	В2
14.CL.7	Кладовая	3,80	В2
14.CL.8	Кладовая	3,80	В2
14.CL.9	Кладовая	3,50	В2
14.CL.10	Кладовая	4,80	В2
14.CL.11	Кладовая	4,70	В2
14.CL.12	Кладовая	5,80	В2
14.CL.13	Кладовая	3,40	В2
14.CL.14	Кладовая	3,60	В2
14.CL.15	Проход	30,10	В2
		91,30	
Блок кладовых под аренду -03.CL.15			
15.CL.1	Кладовая под аренду	2,70	В2
15.CL.2	Кладовая под аренду	2,70	В2
15.CL.3	Кладовая под аренду	3,00	В2
15.CL.4	Кладовая под аренду	2,50	В2
15.CL.5	Кладовая под аренду	2,50	В2
15.CL.6	Кладовая под аренду	2,60	В2
15.CL.7	Кладовая под аренду	3,30	В2
15.CL.8	Кладовая под аренду	3,30	В2
15.CL.9	Кладовая под аренду	3,30	В2
15.CL.10	Кладовая под аренду	3,30	В2
15.CL.11	Кладовая под аренду	3,30	В2
15.CL.12	Кладовая под аренду	3,50	В2
15.CL.13	Кладовая под аренду	3,50	В2
15.CL.14	Кладовая под аренду	3,50	В2
15.CL.15	Кладовая под аренду	3,20	В2
15.CL.16	Кладовая под аренду	3,20	В2
15.CL.17	Кладовая под аренду	3,50	В2
15.CL.18	Кладовая под аренду	2,60	В2
15.CL.19	Кладовая под аренду	2,70	В2
15.CL.20	Кладовая под аренду	2,70	В2
15.CL.21	Кладовая под аренду	2,70	В2
15.CL.22	Кладовая под аренду	3,40	В2
15.CL.23	Кладовая под аренду	2,80	В2
15.CL.24	Кладовая под аренду	2,80	В2
15.CL.25	Кладовая под аренду	6,30	В2
15.CL.26	Кладовая под аренду	3,20	В2
15.CL.27	Кладовая под аренду	3,40	В2
15.CL.28	Кладовая под аренду	2,80	В2
15.CL.29	Кладовая под аренду	2,80	В2
15.CL.30	Проход	57,40	В2
		148,50	
Блок кладовых под аренду -03.CL.16			
16.CL.1	Кладовая под аренду	4,60	В2
16.CL.2	Кладовая под аренду	2,50	В2
16.CL.3	Кладовая под аренду	5,10	В2
16.CL.4	Кладовая под аренду	3,50	В2
16.CL.5	Проход	7,30	В2
16.CL.6	Кладовая под аренду	2,50	В2
		25,50	
Блок кладовых под аренду -03.CL.17			
17.CL.1	Кладовая под аренду	4,20	В2
17.CL.2	Кладовая под аренду	2,90	В2
17.CL.3	Кладовая под аренду	2,90	В2
17.CL.4	Кладовая под аренду	3,70	В2
17.CL.5	Кладовая под аренду	3,80	В2
17.CL.6	Кладовая под аренду	3,80	В2
17.CL.7	Кладовая под аренду	3,80	В2
17.CL.8	Кладовая под аренду	4,40	В2
17.CL.9	Кладовая под аренду	4,40	В2
17.CL.10	Кладовая под аренду	4,60	В2
17.CL.11	Кладовая под аренду	5,10	В2
17.CL.12	Кладовая под аренду	2,50	В2
17.CL.13	Кладовая под аренду	2,60	В2
17.CL.14	Кладовая под аренду	2,60	В2
17.CL.15	Кладовая под аренду	2,90	В2
17.CL.16	Кладовая под аренду	4,20	В2
17.CL.17	Кладовая под аренду	4,10	В2
17.CL.18	Кладовая под аренду	4,20	В2
17.CL.19	Кладовая под аренду	4,10	В2
17.CL.20	Кладовая под аренду	4,10	В2
17.CL.21	Кладовая под аренду	4,30	В2
17.CL.22	Кладовая под аренду	4,30	В2
17.CL.23	Кладовая под аренду	4,30	В2
17.CL.24	Кладовая под аренду	4,20	В2
17.CL.25	Кладовая под аренду	5,10	В2
17.CL.26	Кладовая под аренду	3,10	В2
17.CL.27	Кладовая под аренду	3,30	В2
17.CL.28	Кладовая под аренду	3,30	В2
17.CL.29	Кладовая под аренду	3,30	В2
17.CL.30	Проход	54,60	В2
		164,70	
Блок кладовых под аренду -03.CL.18			
18.CL.1	Кладовая под аренду	4,20	В2
18.CL.2	Кладовая под аренду	4,20	В2
18.CL.3	Кладовая под аренду	4,30	В2
18.CL.4	Кладовая под аренду	3,20	В2
18.CL.5	Кладовая под аренду	3,20	В2
18.CL.6	Кладовая под аренду	4,90	В2
18.CL.7	Кладовая под аренду	4,70	В2
18.CL.8	Кладовая под аренду	4,90	В2
18.CL.9	Кладовая под аренду	5,80	В2
18.CL.10	Кладовая под аренду	4,40	В2
18.CL.11	Кладовая под аренду	7,00	В2
18.CL.12	Кладовая под аренду	6,40	В2
18.CL.13	Кладовая под аренду	5,90	В2
18.CL.14	Кладовая под аренду	6,20	В2
18.CL.15	Проход	30,50	В2
		99,80	
Блок кладовых -03.CL.19			
19.CL.1	Кладовая	3,40	В2
19.CL.2	Кладовая	3,20	В2
19.CL.3	Кладовая	3,20	В2
19.CL.4	Кладовая	3,20	В2
19.CL.5	Кладовая	3,20	В2
19.CL.6	Кладовая	4,00	В2
19.CL.7	Кладовая	4,00	В2
19.CL.8	Кладовая	4,00	В2
19.CL.9	Кладовая	2,70	В2
19.CL.10	Кладовая	2,70	В2
19.CL.11	Кладовая	3,70	В2
19.CL.12	Кладовая	3,30	В2
19.CL.13	Кладовая	3,20	В2
19.CL.14	Кладовая	3,20	В2
19.CL.15	Кладовая	3,20	В2
19.CL.16	Кладовая	3,20	В2
19.CL.17	Кладовая	2,80	В2
19.CL.18	Кладовая	3,40	В2
19.CL.19	Кладовая	3,20	В2
19.CL.20	Кладовая	3,40	В2
19.CL.21	Кладовая	3,40	В2
19.CL.22	Кладовая	3,40	В2
19.CL.23	Кладовая	3,20	В2
19.CL.24	Кладовая	5,90	В2
19.CL.25	Кладовая	3,30	В2
19.CL.26	Кладовая	5,10	В2
19.CL.27	Кладовая	3,00	В2
19.CL.28	Кладовая	2,90	В2
19.CL.29	Кладовая	3,00	В2
19.CL.30	Кладовая	3,00	В2
19.CL.31	Кладовая	3,00	В2
19.CL.32	Кладовая	2,90	В2
19.CL.33	Кладовая	3,00	В2
19.CL.34	Проход	72,80	В2
		184,10	
Блок кладовых под аренду -03.CL.20			
20.CL.1	Кладовая под аренду	2,80	В2
20.CL.2	Кладовая под аренду	2,80	В2
20.CL.3	Кладовая под аренду	2,80	В2
20.CL.4	Кладовая под аренду	2,70	В2
20.CL.5	Кладовая под аренду	2,70	В2
20.CL.6	Кладовая под аренду	2,80	В2
20.CL.7	Кладовая под аренду	2,80	В2
20.CL.8	Кладовая под аренду	2,80	В2
20.CL.9	Кладовая под аренду	2,80	В2
20.CL.10	Кладовая под аренду	2,80	В2
20.CL.11	Кладовая под аренду	2,90	В2
20.CL.12	Кладовая под аренду	2,90	В2
20.CL.13	Кладовая под аренду	2,90	В2
20.CL.14	Кладовая под аренду	2,90	В2
20.CL.15	Кладовая под аренду	2,90	В2
20.CL.16	Кладовая под аренду	3,90	В2
20.CL.17	Кладовая под аренду	4,00	В2
20.CL.18	Кладовая под аренду	3,00	В2
20.CL.19	Кладовая под аренду	2,90	В2
20.CL.20	Кладовая под аренду	2,90	В2
20.CL.21	Кладовая под аренду	3,00	В2
20.CL.22	Кладовая под аренду	5,50	В2
20.CL.23	Кладовая под аренду	5,20	В2
20.CL.24	Кладовая под аренду	4,00	В2
20.CL.25	Кладовая под аренду	4,00	В2
20.CL.26	Кладовая под аренду	3,00	В2
20.CL.27	Кладовая под аренду	2,90	В2
20.CL.28	Кладовая под аренду	2,90	В2
20.CL.29	Кладовая под аренду	3,00	В2
20.CL.30	Кладовая под аренду	2,50	В2
20.CL.31	Кладовая под аренду	2,50	В2
20.CL.32	Кладовая под аренду	2,50	В2
20.CL.33	Кладовая под аренду	2,50	В2
20.CL.34	Кладовая под аренду	2,50	В2
20.CL.35	Кладовая под аренду	3,70	В2
20.CL.36	Кладовая под аренду	3,80	В2
20.CL.37	Кладовая под аренду	4,50	В2
20.CL.38	Кладовая под аренду	4,50	В2
20.CL.39	Проход	57,80	В2
20.CL.42	Кладовая под аренду	3,30	В2
20.CL.43	Кладовая под аренду	3,30	В2
20.CL.44	Кладовая под аренду	2,10	В2
20.CL.49	Проход	4,20	В2
		192,20	
Блок кладовых -03.CL.21			
21.CL.1	Кладовая	5,70	В2
21.CL.2	Кладовая	6,70	В2
21.CL.3	Кладовая	3,10	В2
21.CL.4	Кладовая	3,00	В2
21.CL.5	Кладовая	3,20	В2
21.CL.6	Кладовая	2,70	В2
21.CL.7	Кладовая	2,90	В2
21.CL.8	Кладовая	2,90	В2
21.CL.9	Кладовая	3,90	В2
21.CL.10	Кладовая	3,90	В2
21.CL.11	Кладовая	3,50	В2
21.CL.12	Кладовая	3,80	В2
21.CL.13	Кладовая	3,50	В2
21.CL.14	Кладовая	3,80	В2
21.CL.15	Кладовая	3,90	В2
21.CL.16	Кладовая	4,20	В2
21.CL.17	Кладовая	4,90	В2
21.CL.18	Кладовая	3,70	В2
21.CL.19	Кладовая	3,70	В2
21.CL.20	Кладовая	3,60	В2
21.CL.21	Кладовая	3,70	В2
21.CL.22	Кладовая	3,70	В2
21.CL.23	Кладовая	3,60	В2
21.CL.24	Кладовая	4,10	В2
21.CL.25	Кладовая	6,50	В2
21.CL.26	Проход	49,90	В2
		148,10	
Блок кладовых под аренду -03.CL.22			
22.CL.1	Кладовая под аренду	5,60	В2
22.CL.2	Кладовая под аренду	4,70	В2
22.CL.3	Кладовая под аренду	4,70	В2
22.CL.4	Кладовая под аренду	4,70	В2
22.CL.5	Кладовая под аренду	4,70	В2
22.CL.6	Кладовая под аренду	4,60	В2
22.CL.7	Кладовая под аренду	5,30	В2
22.CL.8	Кладовая под аренду	5,20	В2
22.CL.9	Кладовая под аренду	5,20	В2
22.CL.10	Кладовая под аренду	5,20	В2
22.CL.11	Кладовая под аренду	4,80	В2
22.CL.12	Кладовая под аренду	4,20	В2
22.CL.13	Проход	15,00	В2
		73,90	
Блок кладовых под аренду -03.CL.23			
23.CL.1	Кладовая под аренду	4,20	В2
23.CL.2	Кладовая под аренду	3,10	В2
23.CL.3	Кладовая под аренду	3,10	В2
23.CL.4	Кладовая под аренду	3,10	В2
23.CL.5	Кладовая под аренду	2,90	В2
23.CL.6	Кладовая под аренду	4,60	В2
23.CL.7	Кладовая под аренду	4,00	В2
23.CL.8	Кладовая под аренду	3,40	В2
23.CL.9	Кладовая под аренду	3,40	В2
23.CL.10	Кладовая под аренду	3,40	В2
23.CL.11	Кладовая под аренду	2,90	В2
23.CL.12	Кладовая под аренду	3,80	В2
23.CL.13	Кладовая под аренду	3,50	В2
23.CL.14	Проход	22,60	В2
		68,00	
Блок кладовых под аренду -03.CL.24			
24.CL.1	Кладовая под аренду	2,90	В2
24.CL.2	Кладовая под аренду	2,80	В2
24.CL.3	Кладовая под аренду	2,80	В2
24.CL.4	Кладовая под аренду	2,80	В2
24.CL.5	Кладовая под аренду	2,80	В2
24.CL.6	Кладовая под аренду	2,80	В2
24.CL.7	Кладовая под аренду	6,30	В2
24.CL.8	Проход	17,10	В2
		40,30	
Блок кладовых под аренду -03.CL.25			
25.CL.1	Кладовая под аренду	3,80	В2
25.CL.2	Кладовая под аренду	3,80	В2
25.CL.3	Кладовая под аренду	3,80	В2
25.CL.4	Кладовая под аренду	3,80	В2
25.CL.5	Кладовая под аренду	3,90	В2
25.CL.6	Кладовая под аренду	3,30	В2
25.CL.7	Кладовая под аренду	5,00	В2
25.CL.8	Кладовая под аренду	3,50	В2
25.CL.9	Кладовая под аренду	3,90	В2
25.CL.10	Кладовая под аренду	3,90	В2
25.CL.11	Кладовая под аренду	3,90	В2
25.CL.12	Кладовая под аренду	3,90	В2
25.CL.13	Кладовая под аренду	3,30	В2
25.CL.14	Кладовая под аренду	3,60	В2
25.CL.15	Проход	18,80	В2
		72,20	
		1643,90	

Экспликация помещений МОП -3 этажа

№ пом.	Наименование	Площадь, м²	Кат. пом.
МОП			
-03.C0.22	Лифтовой холл (тамбур-шлюз)	31,00	
-03.C0.23	ЛК №0.8 (Н2)	18,50	
-03.C0.26	Переход (тамбур-шлюз)	6,30	
-03.C0.27	ЛК №0.1.2 (Н3)	24,20	
-03.C0.28	ЛК №0.1.3 (Н3)	19,30	
-03.C0.29	Переход (тамбур-шлюз)	5,40	
-03.C0.30	Лифтовой холл (тамбур-шлюз)	29,20	
-03.C0.31	Колясочная	16,80	В3
-03.C0.32	Лифтовой холл (тамбур-шлюз)	17,40	
-03.C0.33	ЛК №0.9 (Н2)	17,70	
-03.C0.34	Лифтовой холл (тамбур-шлюз)	22,10	
-03.C0.35	ЛК №0.10 (Н2)	19,40	
-03.C0.36	Лифтовой холл (тамбур-шлюз)	17,00	
-03.C0.37	Лифтовой холл (тамбур-шлюз)	13,10	
-03.C0.38	ЛК №0.11 (Н2)	19,80	
-03.C0.39	Лифтовой холл (тамбур-шлюз)	55,20	
-03.C0.40	Колясочная	14,60	В3
-03.C0.41	ЛК №0.12 (Н2)	20,80	
-03.C0.42	Лифтовой холл (тамбур-шлюз)	27,60	
-03.C0.43	Колясочная	13,20	В3
-03.C0.44	Лифтовой холл (тамбур-шлюз)	24,60	
-03.C0.45	Колясочная	11,30	В3
-03.C0.46	Лифтовой холл (тамбур-шлюз)	21,40	
-03.C0.47	Колясочная	18,90	В3
-03.C0.48	Лифтовой холл (тамбур-шлюз)	39,50	
-03.C0.49	Колясочная	14,50	В3
-03.C0.50	Лифтовой холл (тамбур-шлюз)	10,80	
-03.C0.51	Лифтовой холл (тамбур-шлюз)	30,20	
-03.C0.52	Колясочная	18,00	В3
-03.C0.53	ЛК №0.15 (Н3)	20,50	
		618,30	
Подземная автостоянка			
-03.P.5	Помещение для хранения автомобилей	17437,20	В2
		17437,20	
Служебные помещения			
-03.S0.9	Помещение персонала	11,10	
-03.S0.10	Санузел персонала	5,90	
-03.S0.11	Помещение персонала	14,90	
-03.S0.12	Санузел персонала	4,20	
-03.S0.13	Санузел персонала	4,30	
-03.S0.14	Помещение персонала	12,60	
-03.S0.15	Санузел персонала	3,60	
-03.S0.16	Помещение персонала	11,30	
-03.S0.17	Санузел персонала	4,70	
-03.S0.18	Помещение персонала	10,00	
		82,60	
Технические помещения			
-03.T0.65	КНС	39,90	Д
-03.T0.66	Электрощитовая жилья	38,30	В2
-03.T0.67	Помещение СС	17,30	В3
-03.T0.68	Электрощитовая жилья	21,50	В2
-03.T0.69	Электрощитовая торговых помещений	19,70	В2
-03.T0.70	Электрощитовая жилья	25,60	В2
-03.T0.71	КНС	32,60	Д
-03.T0.72	Помещение СС	13,20	В3
-03.T0.73	Венткамера (автостоянка П, КДУ Секция 6)	122,80	В2
-03.T0.74	Венткамера (торговые помещения ПВ 3 этап)	100,40	Д
-03.T0.75	Электрощитовая торговых помещений	21,50	В2
-03.T0.76	КНС	40,40	Д
-03.T0.77	Электрощитовая жилья	31,90	В2
-03.T0.79	Венткамера (вестибюль ДУ)	16,90	Д
-03.T0.80	Венткамера (автостоянка П 3 этап)	247,70	В2
-03.T0.81	Венткамера (автостоянка В Секция 5,9)	95,90	В2
-03.T0.82	Венткамера (автостоянка П, КДУ Секция 6)	64,20	В2
-03.T0.83	Венткамера (автостоянка П, КДУ Секция 6)	57,00	В2
-03.T0.84	Венткамера (автостоянка ДУ Секция 5,9)	30,00	В2
-03.T0.85	Венткамера (автостоянка В Секция 6)	44,20	В2
-03.T0.86	Венткамера (автостоянка ДУ Секция 7)	39,40	В2
-03.T0.87	Электрощитовая торговых помещений	27,20	В2
-03.T0.88	КНС	54,40	Д
-03.T0.89	Электрощитовая жилья	35,10	В2
-03.T0.90	Помещение СС	20,60	В3
-03.T0.91	Венткамера (автостоянка П, КДУ Секция 7)	86,70	В2
-03.T0.92	КНС	25,30	Д
-03.T0.93	Помещение СС	26,40	В3
-03.T0.94	Помещение СС	16,40	В3
-03.T0.95	Электрощитовая автостоянки	22,70	В2
-03.T0.96	Венткамера (автостоянка П, КДУ Секция 11)	133,20	В2
-03.T0.97	КНС	41,20	Д
-03.T0.98	Холодильный центр	613,90	В2
-03.T0.99	Электрощитовая жилья	36,00	В2
-03.T0.101	Трансформ. камера	10,90	В3
-03.T0.102	Помещение распред. устройства	6,30	В3
-03.T0.104	Трансформ. камера	10,90	В3
-03.T0.105	Помещение распред. устройства	6,50	В3
-03.T0.107	Трансформ. камера	10,90	В3
-03.T0.109	Трансформ. камера	10,90	В3
-03.T0.110	Помещение СС	22,10	В3
-03.T0.111	ГРЩ 7	42,40	В2
-03.T0.112	ГРЩ 8	38,80	В2
-03.T0.143	Венткамера	18,60	В2
-03.T0.144	Помещение УУТЭ	28,50	В2
-03.T0.145	Венткамера (автостоянка В Секция 5,9)	25,10	В2
-03.T0.146	Венткамера	31,30	В2
-03.T0.147	Помещение УУТЭ	18,10	В2
-03.T0.148	Венткамера	26,80	В2
-03.T0.149	Венткамера	25,50	В2
-03.T0.150	Помещение УУТЭ	22,30	В2
-03.T0.151	Венткамера	26,10	В2
-03.T0.152	Помещение УУТЭ	22,30	В2
-03.T0.153	Венткамера	31,00	В2
-03.T0.154	Венткамера	12,50	В2
-03.T0.155	Венткамера	44,60	В2
-03.T0.156	Венткамера	22,90	В2
-03.T0.157	Помещение распред. устройства	6,30	В3
-03.T0.158	Помещение распред. устройства	6,50	В3
		2787,60	
Уборка мест общего пользования			
-03.Y0.6	Помещение уборочной техники (автостоянка)	9,70	В3
-03.Y0.7	ПУИ (автостоянка)	15,50	В3
		25,20	
Управляющая компания/Инженерная служба			
-03.U0.2	Кладовая ЗИП	15,80	В3
		15,80	
		20966,70	

Изм.	Кол.уч.	Лист	№ док.	Подпись	Дата

1042-Р-3 - ИСХ

«Многофункциональный жилой комплекс с подземной автостоянкой, апартаментами и встроенно-пристроенными нежилыми помещениями, с фрагментарной реставрацией и приспособлением объектов культурного наследия на территории Бадаевского пивоваренного завода, расположенного по адресу: Кутузовский проспект, вл. 12/2, 12/6, 12/3, 12/1, 12/4, 12/5, район Дорогомилово, Западный административный округ города Москвы»

Задания

Стадия	Лист	Листов
Р	7	

План -3-ого этажа

A0x2A